



Length 长度(mm)	Width 宽度(mm)	Height 高度(mm)	Pay Cat. 付款等级	Line 行号	Qty 数量	Mark 构件号	Sub Mark 次构件号	Description 截面尺寸	Material 材质	Length 长度(mm)	Finish 油漆	ABM 材料订单号	Weight 重量(kg)	REMARK 备注
9748	250	335		1	1	BE021		Beam						
1810.02.10.03.12				2	1		BE021	HW250x250x14	Q355B	9704	G		897.04	
1810.02.10.03.12				3	2		p122	PL22x250	Q355B	335	G		28.93	
1810.02.10.03.12				4	2		p123	PL12x85	Q355B	155	G		1.47	
												TOTAL	727.43	



ASSEMBLY BOLT LIST (FOR 1 ASSEMBLY)					
Dia.	Grade	Pay Code	Length	No.	Site/Shop
(Mechanical galvanized only for DTI washer)					

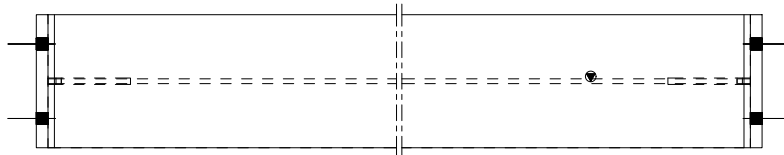

A - A
1:10

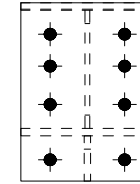

B - B
1:10

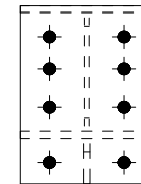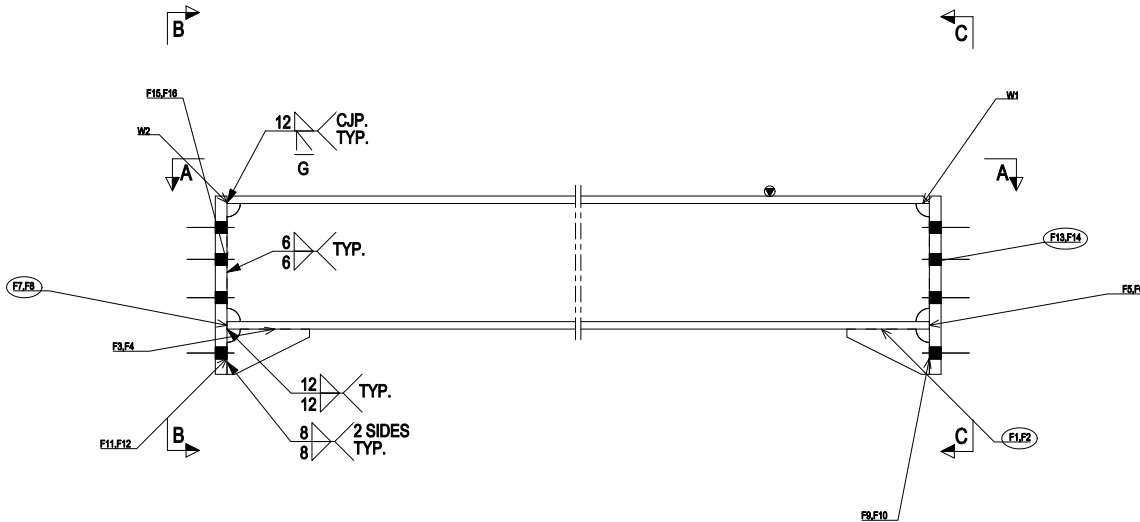

C - C
1:10

1 Beam BE021

1. ACCUMULATIVE DIMENSIONS ARE TAKEN FROM THE "TOP" LINE. 累积尺寸系从顶部线 "TOP" 开始计算。
2. ALL GAS REPAIRS MUST BE WELDED WITH A MINIMUM OF 1mm U.G.O. 所有气焊修复必须采用 1mm 以上 U.G.O. 进行。
3. ALL DIMENSIONS THIS SHEET TO BE PREPARED Q355B-S-01 1. 本图所有尺寸均按 Q355B-S-01 1. 进行。
4. ASSEMBLY MARK TO BE STAMPED ON THE FACE WHERE INDICATED THERE. 构件号打钢印 标注在面上。
5. "X" INDICATES THE TOUCH FACE OF MEMBERS. SHIP ALIEN SPOT THERE. "X" 标注在接触面。船外点在此处。
6. ALL THE DIAMETER OF SCALLOP IS 25mm U.G.O. 所有圆角半径必须为 25mm U.G.O. 标注在图中。
7. ALL WELDS SHALL BE CONTINUOUS U.G.O. 所有焊缝必须连续 U.G.O. 标注在图中。
8. REAL WELDS OF 3MM FILLET WELD SHALL BE PROVIDED IN WELDED CONNECTIONS. 所有节点必须采用 3mm 角焊缝。
9. TOPPOWER BOLTS SHALL BE RED COATED TO CORROSION FROM THE PERMANENT MOIST. 顶部螺栓必须涂红漆防腐。

00	23JUN25	ISSUE FOR FABRICATION	WF	WW	YF	YF
REV	DATE	REVISION	BY	CHKD	APVD	APVD
TEN CCC JV			PURCHASER'S PERMISSION TO PROCEED OR REVIEW TAKEN ON VENDOR PRINTS SHALL NOT RELIEVE VENDOR FROM ITS RESPONSIBILITIES UNDER PURCHASE ORDER.			
RETURN TO VENDOR			RESPOND BY			
☐ 1 REVISE AND RESUBMIT						
☐ 2 TO BE ISSUED AS FINAL PROVIDED COMMENTS ARE INCORPORATED						
☐ 3 NOT COMMENT - FINAL ISSUE						
☐ 4 FOR INFORMATION ONLY						
North Field South Project Onshore LNG Facilities						
QatarEnergy LNG						
THIS DOCUMENT IS PROPERTY OF QATARENERGY LNG. THIS DRAWING OR MATERIAL, DISCLOSED THEREIN MAY NOT BE COPIED OR REPRODUCED IN ANY FORM OR MANNER TO THIS FIRM, OR USED FOR OTHER THAN THE PURPOSE FOR WHICH IT HAS BEEN PROVIDED, IN WHOLE OR IN PART, IN ANY MANNER EXCEPT AS EXPRESSLY PERMITTED BY QATARENERGY LNG.						
UNITED STEEL STRUCTURES LTD.						
COMPANY CONTRACT NO.: LTCGNF5649821			CONTRACTOR JOB NO.: N/A			
P.O.: 215777C008-00000-PO-1800-20301-NFS620						
REQUISITION NO.: NFS_EPC-TECC-ST-REQ-20301						
EQUIPMENT NAME: PACKAGE - III- STEEL STRUCTURES (Offshore Area)						
TAG NO.: 361-RC3210-S-01						
VENDOR NAME: UNITED STEEL STRUCTURES LTD.						
DOCUMENT CLASS: 3						
VENDOR DOCUMENT NO.: ST20301-02048						
TITLE INLET AREA STEEL STRUCTURE DRAWING 361-RC3210-S-01-BE021						
SCALE 1:10		PROJECT NO. LTCGNF5649821				
PROJECT NFS	PROJECT DOCUMENT NO. 5486_21-ST20301-02045	SHEET No. 1	SIZE A3	REVISION 00		

1	A-B/1-2/QNHD +19.000
QTY	MEMBERS LOCATION