



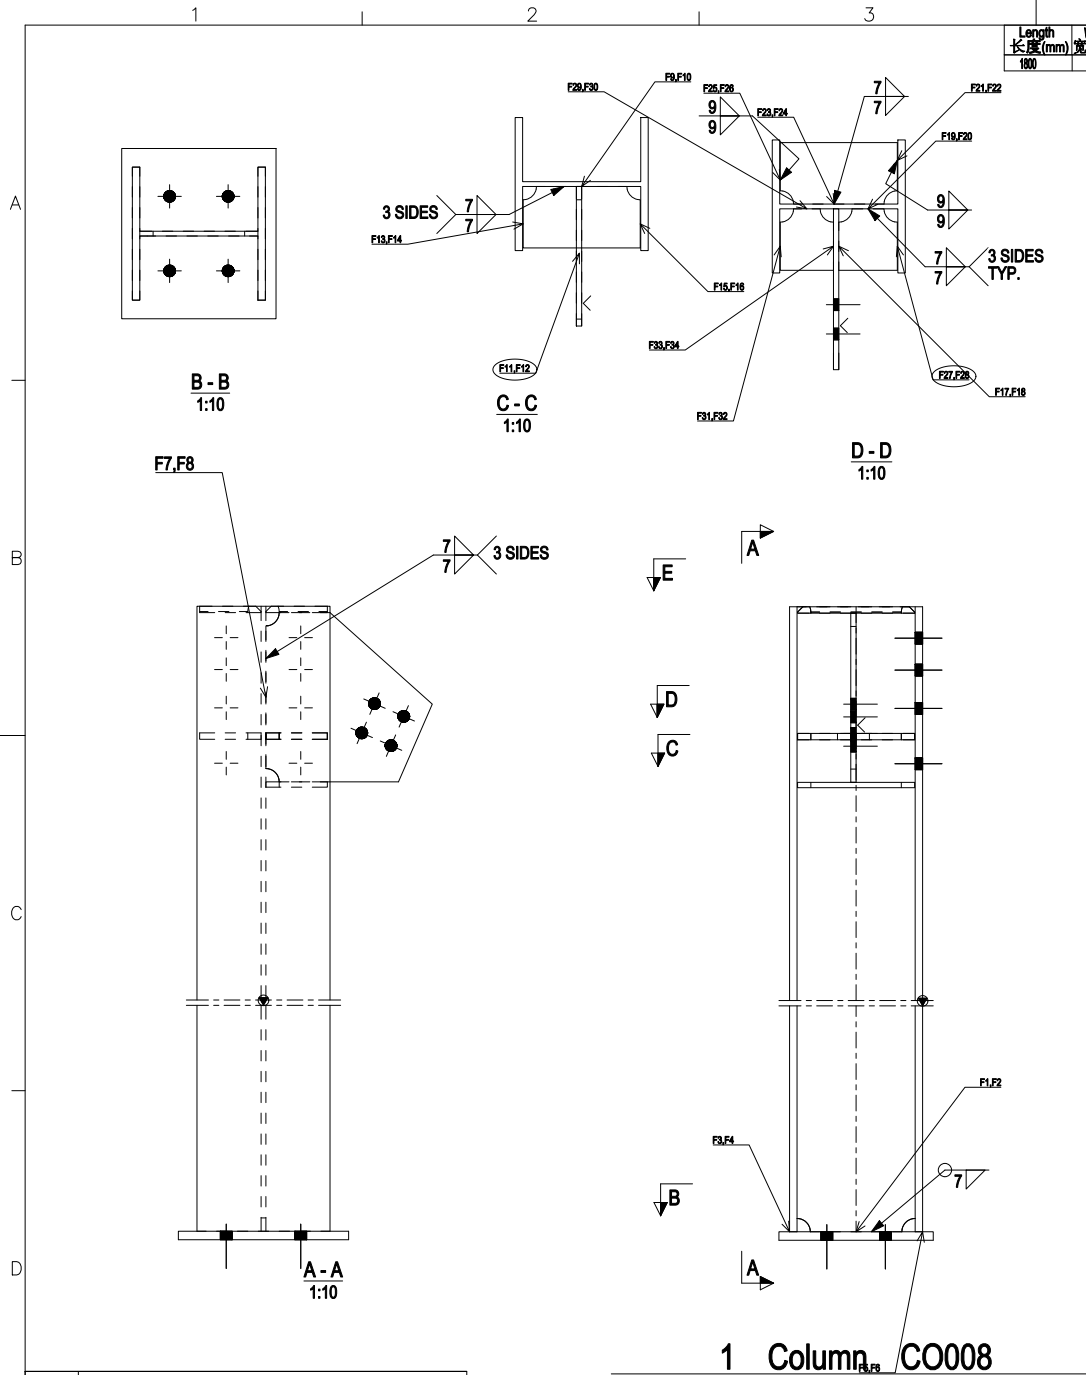

Length 长度(mm)	Width 宽度(mm)	Height 高度(mm)	Pay Cat. 付款等级	Line 行号	Qty. 数量	Mark 构件号	Sub Mark 次构件号	Description 描述尺寸	Material 材质	Length 长度(mm)	Finish 油漆	ABM 材料订单号	Weight 重量(kg)	REMARK 备注
1810.02.10.03.12	2	1	CO008	1	1			Column						
1810.02.10.03.12	2	1		2	1	CO008	CO008	HW250x250x14	Q355B	1784	G		128.13	
1810.02.10.03.12	3	1		3	1	p92		PL16x290	Q355B	320	G		11.66	
1810.02.10.03.12	4	1		4	1	p101		PL10x115.5	Q355B	220	G		1.92	
1810.02.10.03.12	5	1		5	1	p102		PL10x127	Q355B	318	G		6.07	
1810.02.10.03.12	6	2		6	2	p124		PL12x115.5	Q355B	220	G		4.33	
1810.02.10.03.12	7	1		7	1	p125		PL12x115.5	Q355B	220	G		2.30	
1810.02.10.03.12	8	1		8	1	p126		PL12x110	Q355B	116	G		1.10	
1810.02.10.03.12	9	1		9	1	p127		PL12x100	Q355B	116	G		1.00	
TOTAL													158.51	

ASSEMBLY BOLT LIST (FOR 1 ASSEMBLY)					
Dia.	Grade	Pay Code	Length	No.	Site/Shop
20	A325M	G	C1	70	4
20	A325M-DTI	G	C1	75	8

(Mechanical galvanized only for DTI washer)

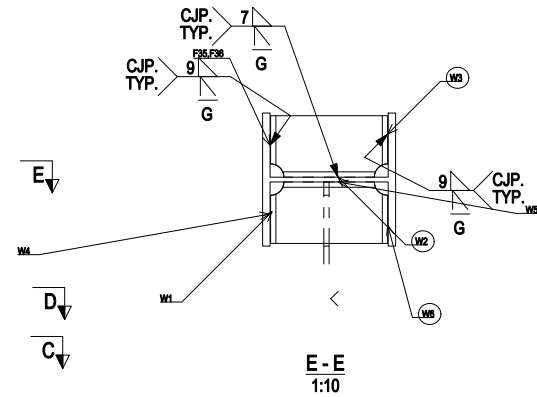

00	23/JUN/25	ISSUE FOR FABRICATION	WF	WW	YF	YF
REV	DATE	REVISION	BY	CHKD	APVD	APVD
RETURN TO VENDOR			RESPOND BY			
☐ 1 REVISE AND RESUBMIT						
☐ 2 TO BE ISSUED AS FINAL PROVIDED COMMENTS ARE INCORPORATED						
☐ 3 NOT COMMENT - FINAL ISSUE						
☐ 4 FOR INFORMATION ONLY						
North Field South Project Onshore LNG Facilities QatarEnergy LNG United Steel Structures Ltd.						
COMPANY CONTRACT NO.: LTCINF5649821			CONTRACTOR JOB NO.: N/A			
P.O.: 215777C008-00000-PO-1800-20301-NFS620						
REQUISITION NO.: NFS_EPC-TECC-ST-REQ-20301						
EQUIPMENT NAME: PACKAGE - III- STEEL STRUCTURES (Offshore Area)						
TAG NO.: 361-RC3210-S-01						
VENDOR NAME: UNITED STEEL STRUCTURES LTD.						
DOCUMENT CLASS: 3						
VENDOR DOCUMENT NO.: ST20301-02048						
STEEL STRUCTURE DRAWING 361-RC3210-S-01-CO008						
SCALE: 1:10			PROJECT NO.: LTCINF5649821			
PROJECT: NFS			PROJECT DOCUMENT NO.: 5496_21-ST20301-02045		SHEET NO.: 1	
					SIZE: A3	
					REVISION: 00	

1. ACCUMULATIVE DIMENSIONS ARE TAKEN FROM THE "TOP" LINE. 累积尺寸系从顶部线 "TOP" 开始计算。
2. ALL DIMENSIONS SHALL HAVE A TOLERANCE OF ±0.5mm UNLESS OTHERWISE SPECIFIED. 除非另有规定, 所有尺寸公差均为 ±0.5mm。
3. ALL DIMENSIONS THIS SHEET TO BE PROVIDED DIMENSIONS SHALL BE PROVIDED DIMENSIONS. 此图上的所有尺寸均为提供尺寸。
4. ASSEMBLY MARK TO BE STAMPED ON THE FACE WHERE INDICATED THEREIN. 构件号行号, 标记在图上。
5. "P" INDICATES THE TOUCH FACE OF MEMBERS, SHIP MUST SPOT THEM. "P" 为构件接触面, 27 需标记在图上。
6. ALL THE DIAMETER OF SCALLOP IS 25mm UNLESS OTHERWISE SPECIFIED. 除非另有规定, 所有圆角直径均为 25mm。
7. ALL WELDS SHALL BE CONTINUOUS UNLESS OTHERWISE SPECIFIED. 除非另有规定, 所有焊缝均为连续焊缝。
8. WELD JOINTS SHALL BE PROVIDED IN WELDED CONNECTIONS. 焊缝接头处应提供在焊接连接处。
9. TYPICAL BOLTS SHALL BE RED COATED TO CORROSION FROM THE PERMANENT MOIST. 典型螺栓应涂红漆, 以防永久锈蚀。