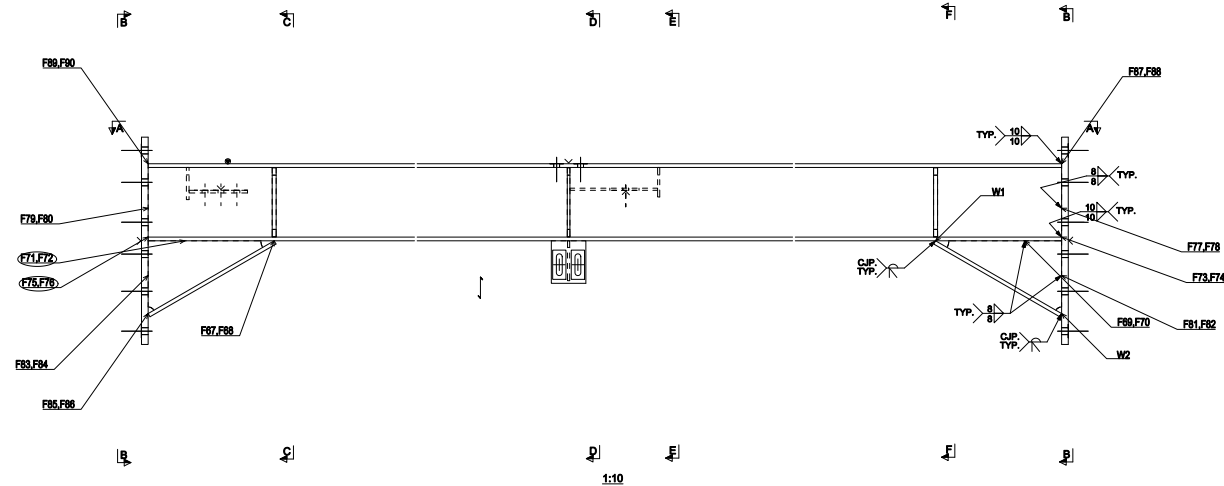
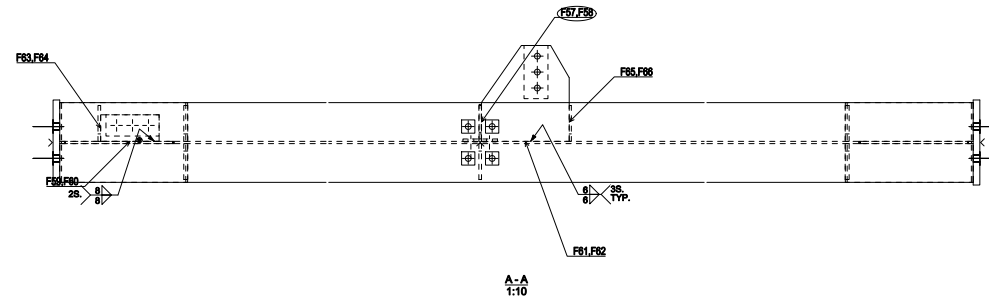


GENERAL NOTES

- Steel structure fabrication shall comply with the requirements of test issue of 4503-AI-OX-10000001
- Unless otherwise specified, fillet welds shall be as per following scheme:

ASSEMBLY TITLE LEGEND			
WELD TYPE	WELD SIZE	WELD ORIENTATION	WELD LOCATION
CHS 1	CHS 2	CHS 3	CHS 4
- Where required, marking area shall be provided on contact surface sides. Unless otherwise specified, marking size and pattern according to below marking details for painting:

CHS 1	CHS 2	CHS 3	CHS 4
CHS 1	CHS 2	CHS 3	CHS 4
- ⊙ denotes assembly orientation mark.
- All dimensions and coordinates are in millimeters, elevations in meters.
- Only within dimension shall be followed, drawing shall not be scaled off.
- Seal welds to be provided as per document 4503-XI-SH-10000001

Part list for one assembly marked: AB0002							Q.ty tot		
TCM Finish 1.Codreproiect: Fireproof							kye:		
Part.N.	Q.ty	Profile	Material	Length [mm]	Weight [kg]	Area [m²]			
				Unit	Total	Unit	Total		
A0190	2	PL20*320	S355J2	235	780	48.98	97.97	0.58	1.1
A0205	1	PL10*130	S355J2	160	1.63	1.63	0.05	0.05	0.05
A0218	1	PL8*130	S355J2	150	0.81	0.81	0.03	0.03	0.03
A0264	2	PL10*135	S355J2	260	2.73	5.46	0.08	0.08	0.15
A0366	1	PL10*121	S355J2	135	1.27	1.27	0.04	0.04	0.04
A0368	4	PL15*135	S355J2	260	4.09	16.37	0.08	0.08	0.32
A0369	2	HEA300	S355J2	548	23.63	47.27	0.94	1.88	1.88
A0370	1	PL8*361	S355J2	330	6.20	6.20	0.2	0.2	0.2
A0372	1	PL10*100	S355J2	220	1.73	1.73	0.05	0.05	0.05
A0374	1	PL8*111	S355J2	135	0.93	0.93	0.03	0.03	0.03
AB0002	1	HEA300	S355J2	5658	499.67	499.67	9.7	9.7	9.7
Assembly total					679.31				13.39

FINISHING SPECIFICATION

Substrate	Surface Preparation	Coating System	DFT (µm)
CS	ISO 8501-1 grade Sa 2.5	A Epoxy FBR	85-105
	ISO 8501-1 grade Sa 2.5	B Polyurethane	100-120
	ISO 8501-1 grade Sa 2.5	C System NCCF (gms)	100

FINISH COAT COLOR

REV.	DATE	ISSUED FOR CONSTRUCTION	Z.Heng	X.Cheng	Z.YingDong
REASON FOR ISSUE			PREPARED	CHECKED	APPROVED
PROJECT TITLE			SILLENNO EPC PE UNITS, LAO AND UI&O		
DRAWING TITLE			INTERCONNECTING PIPE RACK (IPR) SECTION 1 SHOP DRAWING OF BEAM 8901R004010AB0002		
SHEET SIZE A1		PURCHASE ORDER NUMBER 7500137917		REVISION 00	
SCALE 1:10		MATERIAL REQUISITION NUMBER 001T01		SHEET 1 of 1	