
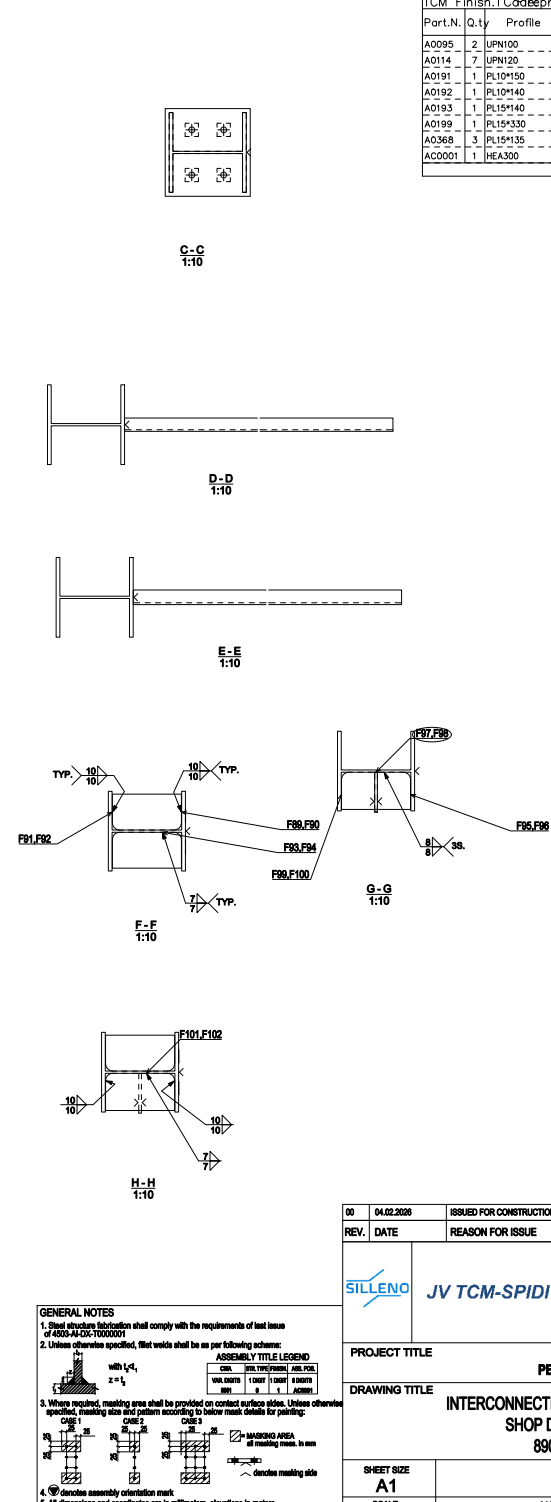
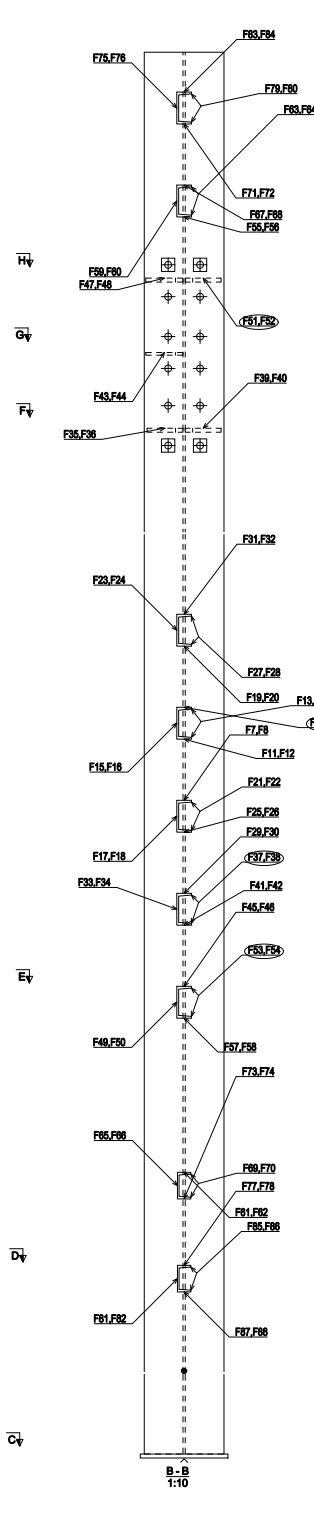


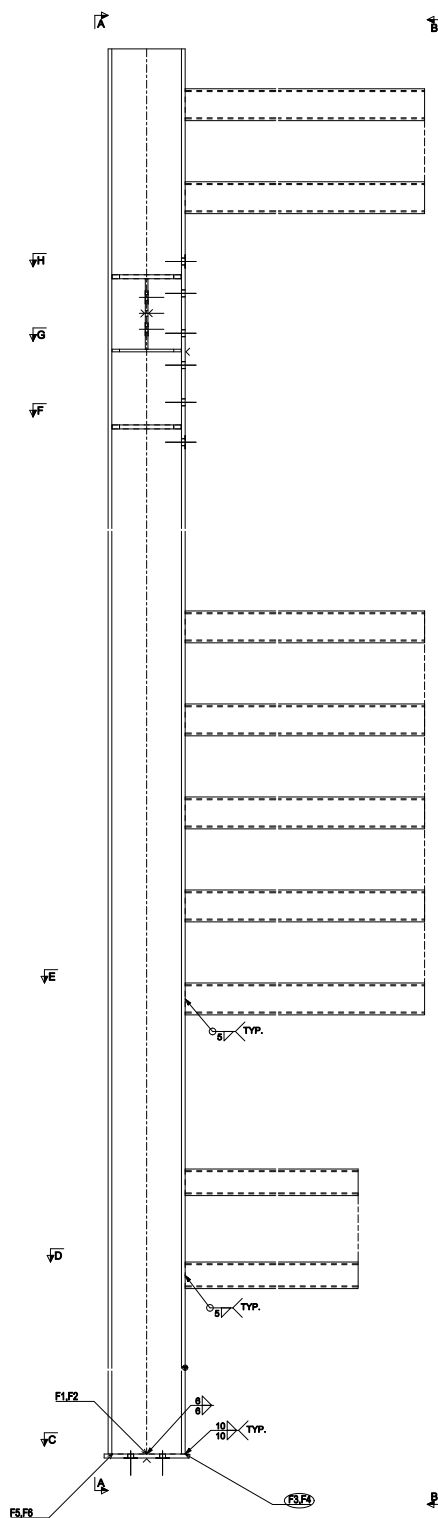

FINISHING SPECIFICATION					
FINISHING CODE	Substrate	Surface Preparation and Joint Profile	Coating System Details	DFT (µm)	
	CS	ISO 8501-1 grade Sa 2.5 SPC-SP 10	A	Epoxy / FBE	80-100
			B	Polyurethane	80-90
			1.2	System HClFT (µm)	160
FINISH COAT COLOR					

00	04.02.2020	ISSUED FOR CONSTRUCTION		Z.Heng	X.Qiang	Z.YingDong
REV.	DATE	REASON FOR ISSUE		PREPARED	CHECKED	APPROVED
   				MANUFACTURER		
				 		
				VENDOR DRAWING No. AC0001		
				DOC. CLARK: 03		
PROJECT TITLE SILLEN EPC PE UNITS, LAO AND UI&O						
DRAWING TITLE INTERCONNECTING PIPE RACK (IPR) SECTION 1 SHOP DRAWING OF COLUMN 8901IR004I01AC0001						
SHEET SIZE A1		PURCHASE ORDER NUMBER 7500137917				REVISION 00
SCALE: 1:10		MATERIAL REQUISITION NUMBER 001T01				SHEET 1 of 1