



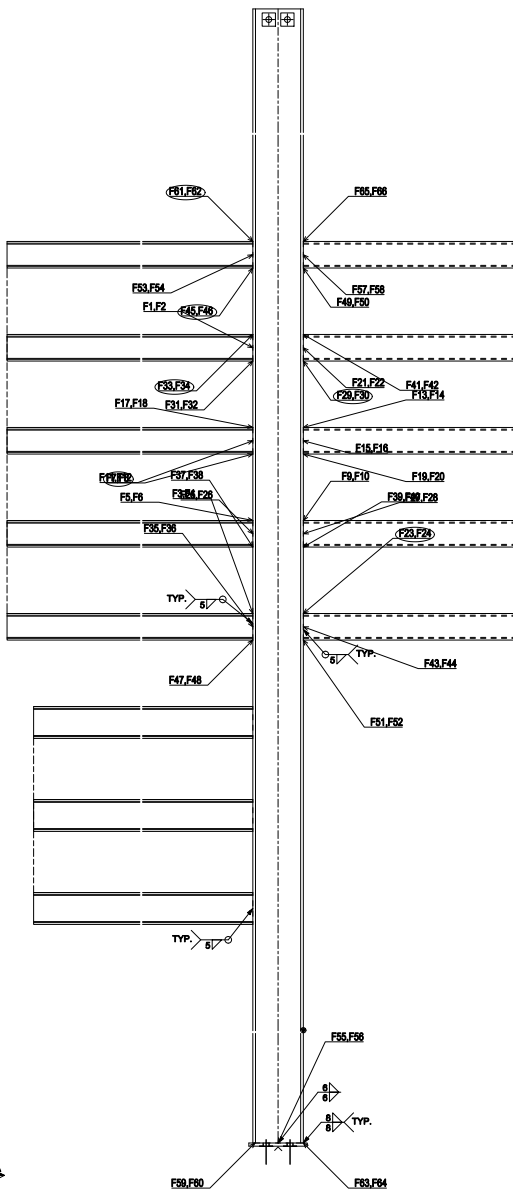

B - B
1:10

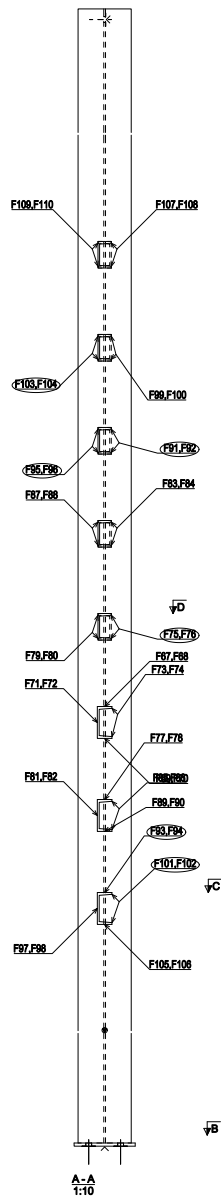

C - C
1:10



D - D
1:10

Part list for one assembly marked: AC0002										Q.ty tot
TCM Finish: 1 Cd Deeproot: 100: Fireproof N/A										
Part.N.	Q.ty	Profile	Material	Length [mm]	Unit	Weight [kg]	Area [m ²]	Unit	Total	
A0008	5	UPN100	S355J2	805		8.53	42.65	0.38	1.50	
A0100	3	UPN120	S355J2	1005		13.41	40.28	0.44	1.3	
A0118	5	UPN100	S355J2	1105		11.71	58.58	0.4	2.04	
A0200	1	PL12*230	S355J2	220		4.77	4.77	0.1	0.1	
AC0002	1	HEA200	S355J2	5398		228.10	228.10	6.13	6.13	
Assembly total									374.11	11.1

FINISHING SPECIFICATION			
Substrate	Surface Preparation and Coat Profile	Coat System Details	DFT (µm)
CS	ISO 8501-1 grade Sa 2.5	A) Spray FBR	85-100
	ISO 8501-1 grade Sa 2.5	B) Polyurethane	100-120
	ISO 8501-1 grade Sa 2.5	C) System HERT (2 coats)	180
FINISH COAT COLOR			

GENERAL NOTES

- Steel structure fabrication shall comply with the requirements of last issue of 4503-AI-00-10000001
- Unless otherwise specified, flat welds shall be as per following scheme:

ASSEMBLY TITLE LEGEND			
WELD TYPE	WELD SIZE	WELD TYPE	WELD SIZE
WELD TYPE	WELD SIZE	WELD TYPE	WELD SIZE
- Where required, marking area shall be provided on contact surface sides. Unless otherwise specified, marking size and pattern according to below mark details for painting:

MARKING AREA	MARKING AREA
MARKING AREA	MARKING AREA
- Ø denotes assembly orientation mark.
- All dimensions and coordinates are in millimeters, elevations in meters.
- Only within dimensions shall be followed, drawing shall not be scaled off.
- Seal welds to be provided as per document 4503-XI-SH-10000001

00	04.02.2026	ISSUED FOR CONSTRUCTION	Z.Heng	X.Cheng	Z.YingDong
REV.	DATE	REASON FOR ISSUE	PREPARED	CHECKED	APPROVED
SILLEN JV TCM-SPIDI TECNIMONT KZ SINOPEC			MANUFACTURER 		
			VENDOR DRAWING No. AC0002 DOC. CLASS: 03		
PROJECT TITLE		SILLEN EPC PE UNITS, LAO AND UI&O			
DRAWING TITLE					
INTERCONNECTING PIPE RACK (IPR) SECTION 1 SHOP DRAWING OF COLUMN 8901IR004101AC0002					
SHEET SIZE A1		PURCHASE ORDER NUMBER 7500137917			REVISION 00
SCALE: 1:10		MATERIAL REQUISITION NUMBER 001T01			SHEET 1 of 1