

Part list for one assembly marked: AT0002 Q.ty tot.

TCM Finish.1 Code: Fireproof Type:


Part.N.	Q.ty	Profile	Material	Lenght [mm]	Weight [kg]		Area [m ²]	
					Unit	Total	Unit	Total
A0210	1	PL15*200	S355J2	280	6.59	6.59	0.13	0.13
AT0002	1	UPN100	S355J2	1129	11.96	11.96	0.42	0.42
Assembly total					18.55			0.55

FINISHING SPECIFICATION


	Substrate	Surface Preparation and Blast Profile	Coat	Generic System Details	DFT (µm)	
PAINTING CYCLE	CS	ISO 8501-1 grade Sa 2.5 or SSPC-SP 10	1.2	A Epoxy / ESI,	80-100	
				B Polyurethane	100-80	
				System NDFT (µm)		180
				FINISH COAT COLOR		



1:10

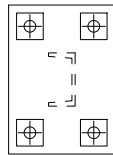

A-A
1:10

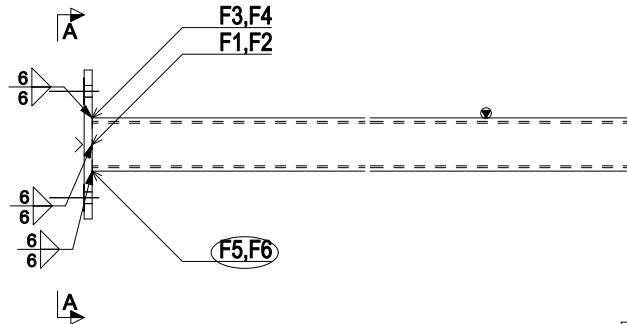


1:10

GENERAL NOTES

1. Steel structure fabrication shall comply with the requirements of last issue of 4503-AI-DX-T0000001

2. Unless otherwise specified, fillet welds shall be as per following scheme:



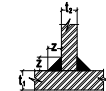


with $t_2 < t_1$
 $z = t_2$

ASSEMBLY TITLE LEGEND

CWA	STR. TYPE	FINISH	ASS. POS.
VAR. DIGITS	1 DIGIT	1 DIGIT	6 DIGITS
8901	0	1	AT0002

3. Where required, masking area shall be provided on contact surface sides. Unless otherwise specified, masking size and pattern according to below mask details for painting:

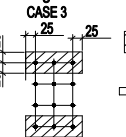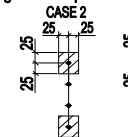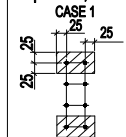

= MASKING AREA
all masking meas. in mm

denotes masking side

4. denotes assembly orientation mark

5. All dimensions and coordinates are in millimeters, elevations in meters

6. Only written dimension shall be followed, drawing shall not be scaled off

7. Seal welds to be provided as per document 4503-XI-SW-T0000001

00	04.02.2026	ISSUED FOR CONSTRUCTION	Z.Neng	X.Qiang	Z.YingDong
REV.	DATE	REASON FOR ISSUE	PREPARED	CHECKED	APPROVED
 JV TCM-SPIDI			TECNIMONT KZ  SINOPEC		
			MANUFACTURER  VENDOR DRAWING No. AT0002		
			DOC. CLASS: 03		
PROJECT TITLE			SILLEN EPC PE UNITS, LAO AND UI&O		
DRAWING TITLE			INTERCONNECTING PIPE RACK (IPR) SECTION 1 SHOP DRAWING OF CABLE TRAY SUPPORT 8901IR004I01AT0002		
SHEET SIZE A3		PURCHASE ORDER NUMBER 7500137917		REVISION 00	
SCALE: 1:10		MATERIAL REQUISITION NUMBER 001T01		SHEET 1 of 1	