




6			7							8				
Length 长度(mm)	Width 宽度(mm)	Height 高度(mm)	Ply Cat. 竹胶板等级	Line 行号	Qty 数量	Mark 构件号	Sub Mark 次构件号	Description 描述	Material 材质	Length 长度 (mm)	Fillet 圆滑	ABM 材料订单号	Weight 重量(kg)	REMARKS 备注
				1		BE018		Broom						
1910.02.10.03.12				2		BE018		HPS30x300r16t5	CNSB	3621	G		357.85	
1910.02.10.03.12				pS2		FL16t16			CNSB	140	G		0.71	
1910.02.10.03.12				4		pS3		FL16t18L4	CNSB	589	G		22.38	
1910.02.10.03.12				5		p18		FL16t20	CNSB	326	G		12.28	
												TOTAL	383.03	

ASSEMBLY BOLT LIST (FOR 1 ASSEMBLY)					
Dia.	Grade	Pay Code	Length	No.	Site/Shop
20	A325M	G	C1	55	6 Site


(Mechanical galvanized only for DTI washer)

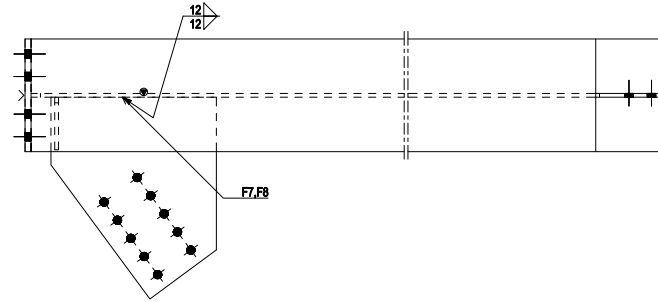

A - A
1:10

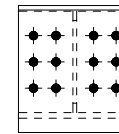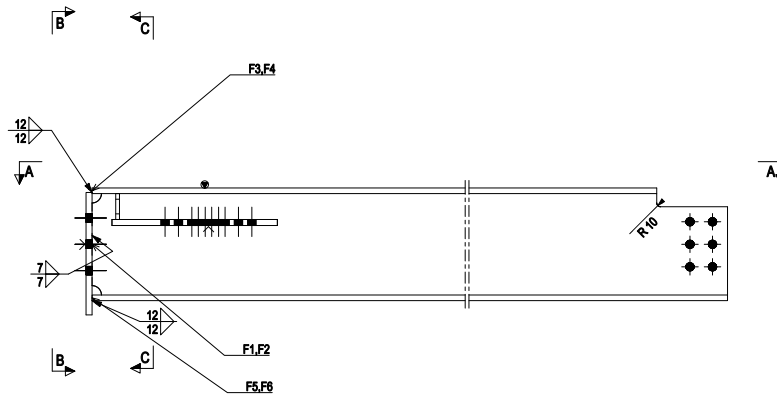

B - E
1:10

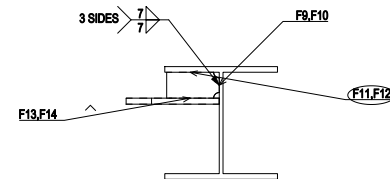

C - C
1:10

00	23-JUN-96	ISSUE FOR FABRICATION	WF S-C-B	WW X-E-R	YF M-B	YF M-B	
REV	DATE	REVISION	BY	CHKD	APVD	APVD	

 PURCHASERS PERMISSION TO PROCEED OR REVIEW THAT THE VENDOR/PRIVATE SHALL NOT HOLD THE VENDOR FROM HIS RESPONSIBILITY UNDER PURCHASE ORDER.	
RETURN TO VENDOR	RESPOND BY
☐ 1 REVISE AND RESUBMIT	_____
☐ 2 TO BE ISSUED AS FINAL PROVIDED COMMENTS ARE INCORPORATED	_____
☐ 3 NOT COMMENT - FINAL ISSUE	_____
☐ 4 FOR INFORMATION ONLY	_____

North Field South Project Onshore LNG Facilities



QatarEnergy LNG



COMPANY CONTRACT NO.:	LYTCGN9569621	CONTRACTOR JOB NO.:	NA
P.O.:	21577K0008-00000-PO-1800-20301-NF8520		
REQUISITION NO.:	NFS_EPC-TECO-ST-REQ-30301		
EQUIPMENT NAME:	PACKAGE - IS-STEELSTRUCTURES (Offsite Area)		
TAG NO.:	361-AC3210-S-01		
VENDOR NAME:	UNITED STEEL STRUCTURES LTD.		
DOCUMENT CLASS:	3		
VENDOR DOCUMENT NO.:	5723001-02046		

TITLE	
INLET AREA	
STEEL STRUCTURE DRAWING	
361-RC3210-S-01-BED18	

SCALE 1:10		PROJECT NO. LTC/GNFB/548021		
PROJECT NFS	PROJECT DOCUMENT NO. 5480_21-ST20301-02045	SHEET No. 1	SIZE A2	REVISION 00

1	A-B/1-2/QNHD +17.200
QTY	MEMBERS LOCATION

1 Beam BE018

1. ALL CUMULATIVE DIMENSIONS ARE TAKEN FROM THE "TOP" LINE. 累积尺寸均按顶部线为基准。
2. ALL 60° OR 90° STEEP CUTS WILL BE A MINIMUM OF 42mm (1 1/2") HIGH. 陡坡切口, 最小高度42mm。
3. ALL SURFACES THIS DIRECTION TO BE PREPARED (S1-4C201-0-0-1) 坡面处理方向为S1-4C201-0-0-1。
4. ASSEMBLY MUST BE STAMPED ON THE BACK WHERE INDICATED THERE. 零件号必须在背面指定位置处。
5. "X" DENOTES THE TOUCH POINT OF MEMBERS. THEY MAY BE SPACED THEM. "X"为接触点, 间距可调整。
6. ALL THE DIAMETER OF BOLLARD IS 22mm (1/2"). 所有螺栓的直径均为22mm。
7. ALL WELDS SHALL BE CONTINUOUS. 所有焊缝必须是连续的。
8. ALL WELDS OF 3MM PLATE THICKNESS SHALL BE PROVIDED BY WELDED CONNECTIONS. 所有厚度为3mm的钢板, 焊缝必须采用焊接连接。
9. TOP SURFACE SHALL BE REQUIRED TO DRAINAGE FROM THE PERIMETER JOINT. 顶面必须能从周边接缝处排水。