
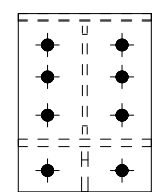
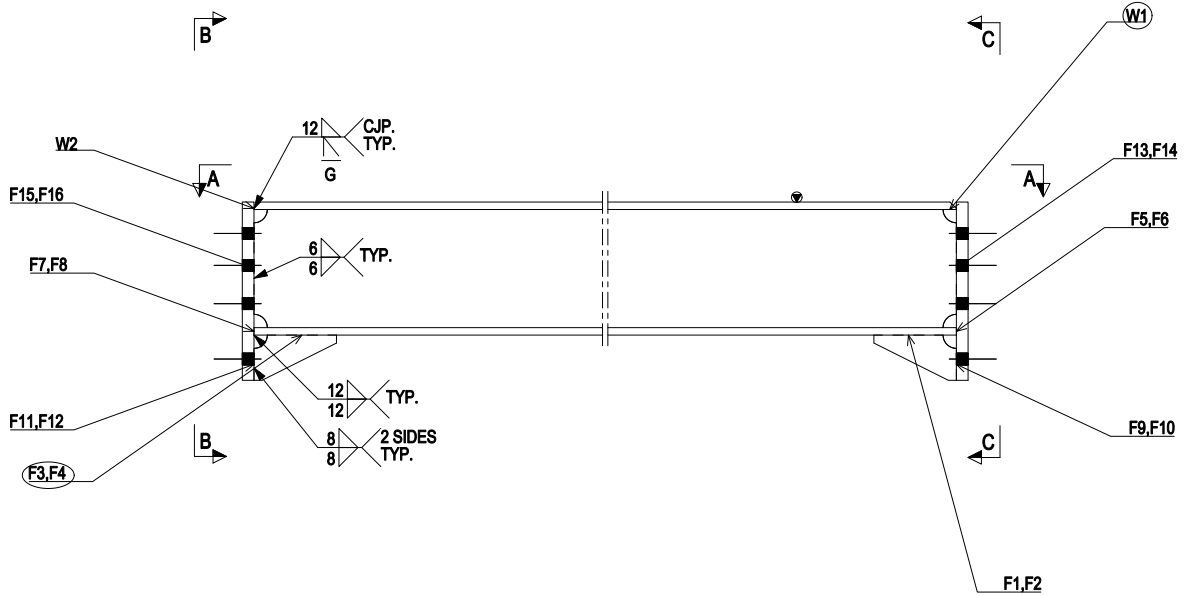
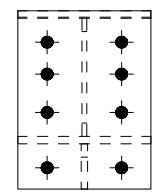


Length 长度(mm)	Width 宽度(mm)	Height 高度(mm)	Pay Cat. 付款等级	Line 行号	Qty 数量	Mark 构件号	Sub Mark 次构件号	Description 截面尺寸	Material 材质	Length 长度(mm)	Finish 油漆	ABM 材料订单号	Weight 重量(kg)	REMARK 备注
9748	250	335		1	1	BE021		Beam						
1810.02.10.03.12				2	1		BE021	HW250x250x14	Q355B	9704	G		897.04	
1810.02.10.03.12				3	2		p122	PL22x250	Q355B	335	G		28.93	
1810.02.10.03.12				4	2		p123	PL12x85	Q355B	155	G		1.47	
												TOTAL	727.43	

ASSEMBLY BOLT LIST (FOR 1 ASSEMBLY)					
Dia.	Grade	Pay Code	Length	No.	Site/Shop
(Mechanical galvanized only for DTI washer)					

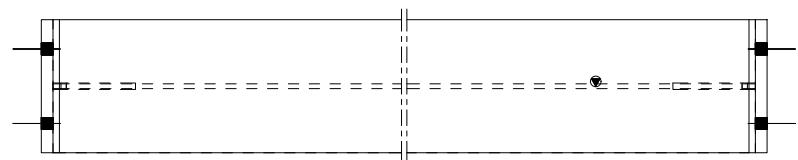

1 Beam BE021

1	A-B/1-2/QNHD +19.000
QTY	MEMBERS LOCATION

1. ACCUMULATIVE DIMENSIONS ARE TAKEN FROM THE "TOP" LINE. 累积尺寸系量至顶部“顶”开始计算。
2. ALL GAS RECOVERY COTS WILL HAVE A RADIUS OF 15mm UNLESS NOTED OTHERWISE. 所有气体回收罐的圆角均为15mm，除非另有说明。
3. ALL DIMENSIONS THIS SHEET TO BE PRECISED Q355B-S-01. 本图所有尺寸均按Q355B-S-01精度。
4. ASSEMBLY MARK TO BE STAMPED ON THE FACE WHERE INDICATED THEREIN. 构件号打钢印，标注在图上。
5. "P" INDICATES THE TOUCH FACE OF MEMBERS, SHIP ALIEN SPOT THEREIN. "P" 标注在图中，表示构件的接触面。
6. ALL THE DIAMETER OF SCALLOP IS 25mm UNLESS NOTED OTHERWISE. 所有圆角半径均为25mm，除非另有说明。
7. ALL WELDS SHALL BE CONTINUOUS, UNLESS NOTED OTHERWISE. 所有焊缝均为连续焊缝，除非另有说明。
8. REAL WELDS OF 3MM FILLET WELD SHALL BE PROVIDED IN WELDED CONNECTIONS. 所有节点处的角焊缝均为3mm角焊缝。
9. TEMPORARY BOLTS SHALL BE RED COATED TO CORROSION FROM THE PERMANENT BOLT. 临时螺栓应涂红漆，以防永久螺栓生锈。

00	23/JUN/25	ISSUE FOR FABRICATION	WF	WW	YF	YF
REV	DATE	REVISION	BY	CHKD	APVD	APVD
RETURN TO VENDOR			RESPOND BY			
☐ 1 REVISE AND RESUBMIT						
☐ 2 TO BE ISSUED AS FINAL PROVIDED COMMENTS ARE INCORPORATED						
☐ 3 NOT COMMENT - FINAL ISSUE						
☐ 4 FOR INFORMATION ONLY						
North Field South Project Onshore LNG Facilities						
QatarEnergy LNG						
THIS DOCUMENT IS PROPERTY OF QATARENERGY LTD. THIS DRAWING OR MATERIAL, DISCLOSED THEREIN MAY NOT BE COPIED OR REPRODUCED IN ANY FORM OR MANNER WITHOUT THE WRITTEN PERMISSION OF QATARENERGY LTD. IF THIS BEEN PROVIDED IN WHOLE OR IN PART IN ANY MANNER EXCEPT AS EXPRESSLY PERMITTED BY QATARENERGY LTD.						
UNITED STEEL STRUCTURES LTD.						
COMPANY CONTRACT NO.:		LTCQNF8549821		CONTRACTOR JOB NO.:		N/A
P.O.:		215777/0008-00000-PO-1800-20301-NFS820				
REQUISITION NO.:		NFS_EPC-TECC-ST-REQ-20301				
EQUIPMENT NAME:		PACKAGE - III- STEEL STRUCTURES (Offshore Area)				
TAG NO.:		361-RC3210-S-01				
VENDOR NAME:		UNITED STEEL STRUCTURES LTD.				
DOCUMENT CLASS:		3				
VENDOR DOCUMENT NO.:		ST20301-02048				
TITLE						
INLET AREA						
STEEL STRUCTURE DRAWING						
361-RC3210-S-01-BE021						
SCALE		1:10		PROJECT NO.		LTCQNF8549821
PROJECT		NFS		PROJECT DOCUMENT NO.		5496_21-ST20301-02045
SHEET No.		1		SIZE		A3
REVISION		00				