
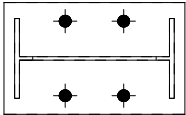


Length 长度(mm)	Width 宽度(mm)	Height 高度(mm)	Pay Cat. 付款等级	Line 行号	Qty 数量	Mark 构件号	Sub Mark 次构件号	Description 描述尺寸	Material 材质	Length 长度(mm)	Finish 油漆	ABM 材料订单号	Weight 重量(kg)	REMARK 备注
2988	210	340		1	1	CO006		Column						
1810.02.10.02.12				2	1		CO006	HN300x150x6.5x8	Q355B	2958	G		108.78	
1810.02.10.02.12				3	1		p33	PL20x210	Q355B	340	G		11.21	
1810.02.10.02.12				4	1		p83	PL20x210	Q355B	340	G		11.21	
												TOTAL	131.20	


ASSEMBLY BOLT LIST (FOR 1 ASSEMBLY)

Dia.	Grade	Pay Code	Length	No.	Site/Shop
20	A325M	G	C1	65	4
20	A325M	G	C1	75	4

(Mechanical galvanized only for DTI washer)

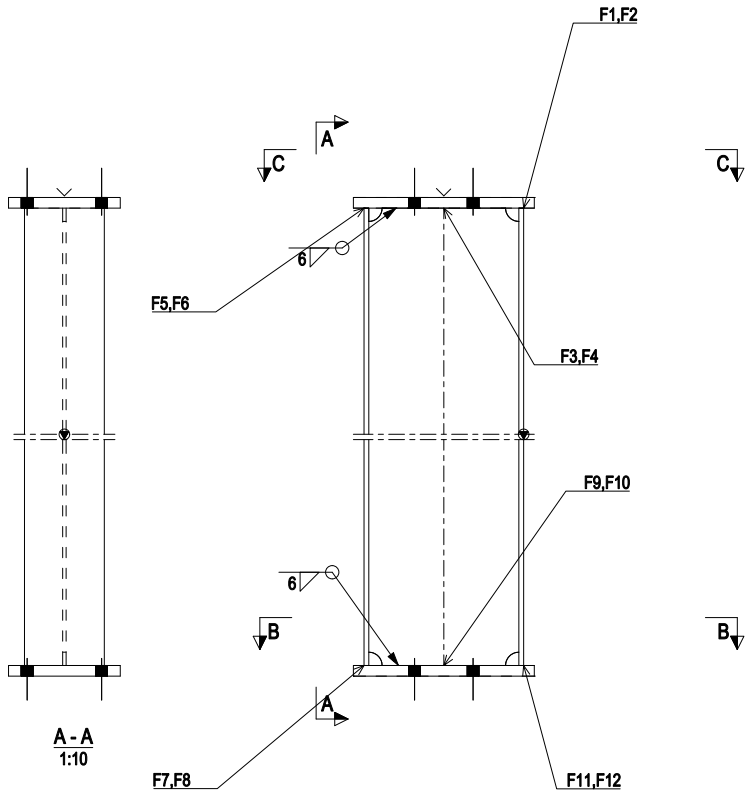

B - B
1:10

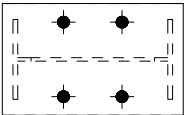

C - C
1:10

1 Column CO006

1	A/1-2/QNHD +16.799
QTY	MEMBERS LOCATION

1. ACCUMULATIVE DIMENSIONS ARE TAKEN FROM THE "TOP" LINE. 累积尺寸系量至顶部 "TOP" 开始计算。
2. ALL DIMENSIONS SHALL HAVE A TOLERANCE OF 1mm UNLESS OTHERWISE SPECIFIED. 所有尺寸公差均为 1mm，除非另有规定。
3. ALL DIMENSIONS THIS SHEET TO BE PROVIDED ON: RC3210-S-01. 本图所有尺寸均需提供在: RC3210-S-01。
4. ASSEMBLY MARK TO BE STAMPED ON THE FACE WHERE INDICATED THEREIN. 构件号打钢印，标注在图上。
5. "P" INDICATES THE TOUCH FACE OF MEMBERS, SHOP MUST SPOT THEM. "P" 为接触面，工厂需打点。
6. ALL THE DIAMETER OF SCALLOP IS 25mm UNLESS OTHERWISE SPECIFIED. 除非另有规定。
7. ALL WELDS SHALL BE CONTINUOUS, UNLESS OTHERWISE SPECIFIED. 除非另有规定。
8. REAL WELDS OF 3MM FILLET WELD SHALL BE PROVIDED IN WELDED CONNECTIONS. 焊接节点处需提供 3mm 角焊缝。
9. TOPWELD BOLTS SHALL BE RED COATED TO CORROSION FROM THE PERMANENT MOIST. 顶部螺栓涂红漆，防腐永久防锈。

00	23JUN25	ISSUE FOR FABRICATION	WF	WW	YF	YF
REV	DATE	REVISION	BY	CHKD	APVD	APVD
RETURN TO VENDOR			RESPOND BY			
☐ 1 REVISE AND RESUBMIT						
☐ 2 TO BE ISSUED AS FINAL PROVIDED COMMENTS ARE INCORPORATED						
☐ 3 NOT COMMENT - FINAL ISSUE						
☐ 4 FOR INFORMATION ONLY						
North Field South Project Onshore LNG Facilities						
QatarEnergy LNG						
THIS DOCUMENT IS PROPERTY OF QATAR ENERGY. IT IS TO BE USED ONLY FOR THE PROJECT AND NOT BE REPRODUCED OR TRANSMITTED IN ANY FORM OR BY ANY MEANS, ELECTRONIC OR MECHANICAL, WITHOUT PERMISSION IN WRITING FROM QATAR ENERGY. IF THIS BEEN PROVIDED IN WHOLE OR IN PART IN ANY MANNER EXCEPT AS EXPRESSLY PERMITTED BY QATAR ENERGY.						
UNITED STEEL STRUCTURES LTD.						
COMPANY CONTRACT NO.: LTCQNFBS649821 CONTRACTOR JOB NO.: N/A						
P.O.: 215777/C008-00000-PO-1800-20301-NFS620						
REQUISITION NO.: NFS_EPC-TECC-ST-REQ-20301						
EQUIPMENT NAME: PACKAGE - III- STEEL STRUCTURES (Offshore Area)						
TAG NO.: 361-RC3210-S-01						
VENDOR NAME: UNITED STEEL STRUCTURES LTD.						
DOCUMENT CLASS: 3						
VENDOR DOCUMENT NO.: ST20301-02048						
TITLE INLET AREA STEEL STRUCTURE DRAWING 361-RC3210-S-01-CO006						
SCALE 1:10		PROJECT NO. LTCQNFBS649821				
PROJECT NFS	PROJECT DOCUMENT NO. 5496_21-ST20301-02045	SHEET No. 1	SIZE A3	REVISION 00		