Length 长度(mm)	Width 宽度(mm)	Height 高度(mm)
1800	477	290

Pay Cat. 付款等级	Line 行号	Qty. 数量	Mark 构件号	Sub Mark 次构件号	Description 截面尺寸	Material 材质	Length 长度(mm)	Finish 油漆	ABM 材料订单号	Weight 重量(kg)	REMARK 备注
	1	1	CO008		Column						
1810.02.10.03.12	2	1		CO008	HW250x250x9x14	Q355B	1784	G		128.13	
1810.02.10.03.12	3	1		p92	PL16x290	Q355B	320	G		11.66	
1810.02.10.03.12	4	1		p101	PL10x115.5	Q355B	220	G		1.92	
1810.02.10.03.12	5	1		p102	PL10x312.7	Q355B	318	G		6.07	
1810.02.10.03.12	6	2		p124	PL12x115.5	Q355B	220	G		4.33	
1810.02.10.03.12	7	1		p125	PL12x115.5	Q355B	220	G		2.30	
1810.02.10.03.12	8	1		p126	PL12x110	Q355B	116	G		1.10	
1810.02.10.03.12	9	1		p127	PL12x100	Q355B	116	G		1.00	
									TOTAL	156.51	

ASSEMBLY BOLT LIST (FOR 1 ASSEMBLY)

Dia.	Grade		Pay Code	Length	No.	Site/Shop
20	A325M	G	C1	70	4	Site
20	A325M-DTI	G	C1	75	8	Site

(Mechanical galvanized only for DTI washer)

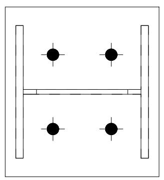

B - B
1:10

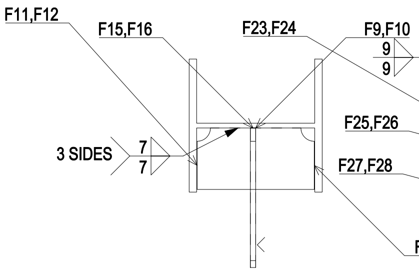

C - C
1:10

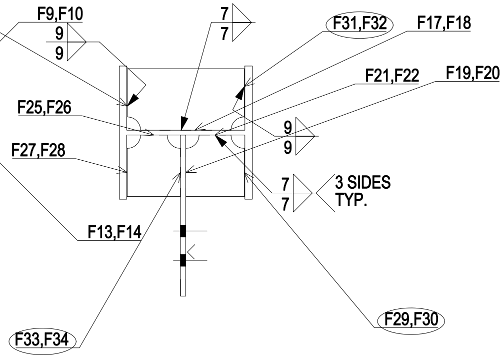

D - D
1:10

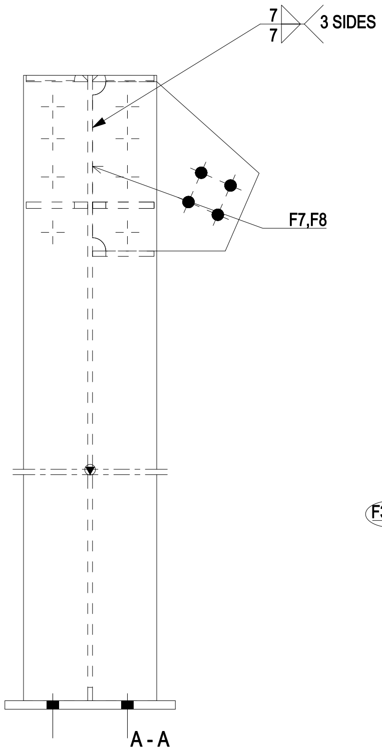

A - A
1:10

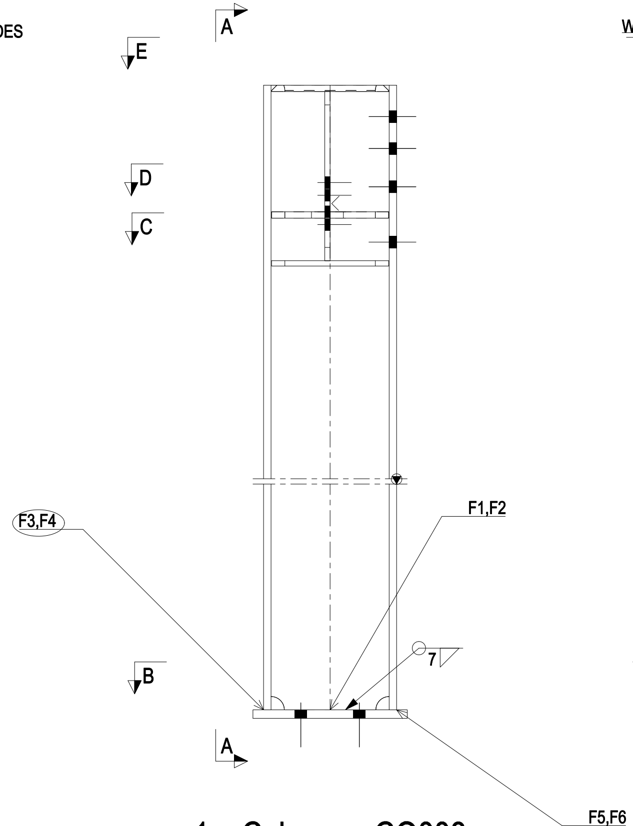

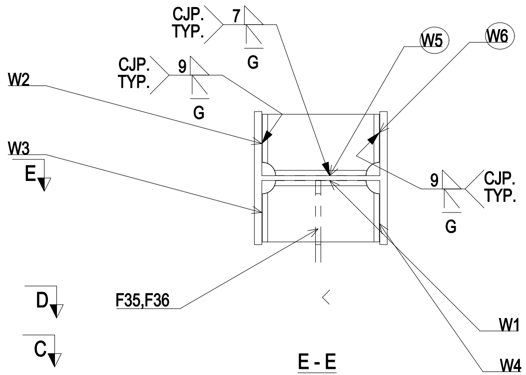

E - E
1:10

1 Column CO008

1	A/1-2/QNHD +19.000
QTY	MEMBERS LOCATION

1. ACCUMULATIVE DIMENSIONS ARE TAKEN FROM THE "RD" LINE. 积累尺寸是根据这线 "RD" 开始计算。
2. ALL GAS RE-ENTRANT CUTS WILL HAVE A RADIUS OF 10mm U.N.O. 所有气割直角切口要有10mm 的半径, 除另有所指。
3. ALL SUBMARKS THIS SHEET TO BE PREFIXED (361-RC3210-S-01). 这张图样的所有副标记前面要加361-RC3210-S-01)。
4. ASSEMBLY MARK TO BE STAMPED ON THE FACE WHERE INDICATED THUS . 构件号打在 标记面上。
5. ">" DENOTES THE TOUCH FACE OF MEMBERS, SHOP MUST SPOT THEM. ">" 为构件结合面, 工厂需标识出来。
6. ALL THE DIAMETER OF SCALLOP IS 25mm U.N.O. 所有扇形倒角半径都是25mm, 除另有所指。
7. ALL WELDS SHALL BE CONTINUOUS, U.N.O. 所有焊缝都是连续焊缝, 除另有所指。
8. SEAL WELDS OF 3MM FILLET WELD SHALL BE PROVIDED IN WELDED CONNECTIONS. 焊接节点里的封焊是3mm角焊缝。
9. TEMPORARY BOLTS SHALL BE RED COATED TO DISTIGUISH FROM THE PERMANENT BOLT. 临时螺栓应涂红油漆, 以区别与永久螺栓。

REV	DATE	REVISION	BY	CHKD	APVD	APVD
00	23JUN25	ISSUE FOR FABRICATION	WYF	WYW	Y.F	Y.F

T.EN CCC JV

PURCHASER'S PERMISSION TO PROCEED OR REVIEW TAKEN ON VENDOR PRINTS SHALL NOT RELIEVE VENDOR FROM ITS RESPONSIBILITIES UNDER PURCHASE ORDER.

RETURN TO VENDOR — RESPOND BY

- ☐ 1 REVISE AND RESUBMIT
- ☐ 2 TO BE ISSUED AS FINAL PROVIDED COMMENTS ARE INCORPORATED
- ☐ 3 NOT COMMENT - FINAL ISSUE
- ☐ 4 FOR INFORMATION ONLY

North Field South Project
Onshore LNG Facilities

QatarEnergy LNG

THIS DOCUMENT IS PROPERTY OF QATARENERGY LNG.THIS DRAWING OR MATERIAL DESCRIBED THEREON MAY NOT BE COPIED OR DISCLOSED IN ANY FORM OR MEDIUM TO THIRD PARTIES, OR USED FOR OTHER THAN THE PURPOSE FOR WHICH IT HAS BEEN PROVIDED, IN WHOLE OR IN PART IN ANY MANNER EXCEPT AS EXPRESSLY PERMITTED BY QATARENERGY LNG.

USSL United Steel Structures,Ltd.

COMPANY CONTRACT NO.: LTC/C/NFS/5496/21 — CONTRACTOR JOB NO.: N/A

P.O: 215777C008-00000-PO-1800-20301-NFS520
REQUISITION NO.: NFS_EPC-TECC-ST-REQ-20301
EQUIPMENT NAME: PACKAGE - III- STEELSTRUCTURES (Offsite Area)
TAG NO.: 361-RC3210-S-01
VENDOR NAME: UNITED STEEL STRUCTURES LTD.
DOCUMENT CLASS: 3
VENDOR DOCUMENT NO.: ST20301-02048

TITLE
INLET AREA
STEEL STRUCTURE DRAWING
361-RC3210-S-01-CO008

SCALE 1:10 — PROJECT NO. LTC/C/NFS/5496/21

PROJECT	PROJECT DOCUMENT NO.	SHEET No.	SIZE	REVISION
NFS	5496_21-ST20301-02045	1	A3	00