



Length 长度(mm)	Width 宽度(mm)	Height 高度(mm)	Pay Cat. 付款等级	Line 行号	Qty 数量	Mark 构件号	Sub Mark 次构件号	Description 截面尺寸	Material 材质	Length 长度(mm)	Finish 油漆	ABM 材料订单号	Weight 重量(kg)	REMARK 备注
9748	250	335		1	1	BE021		Beam						
1810.02.10.03.12				2	1		BE021	HW250x250x14	Q355B	9704	G		897.04	
1810.02.10.03.12				3	2		p122	PL22x250	Q355B	335	G		28.93	
1810.02.10.03.12				4	2		p123	PL12x85	Q355B	155	G		1.47	
												TOTAL	727.43	



ASSEMBLY BOLT LIST (FOR 1 ASSEMBLY)					
Dia.	Grade	Pay Code	Length	No.	Site/Shop
(Mechanical galvanized only for DTI washer)					

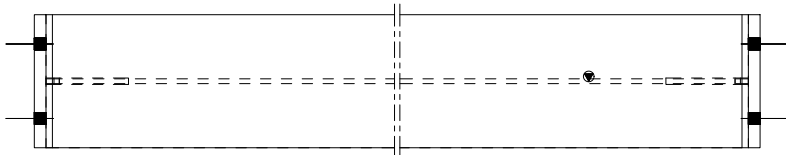

A - A
1:10

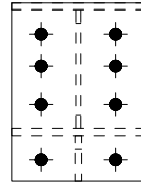

B - B
1:10

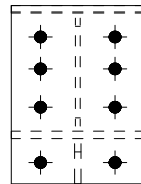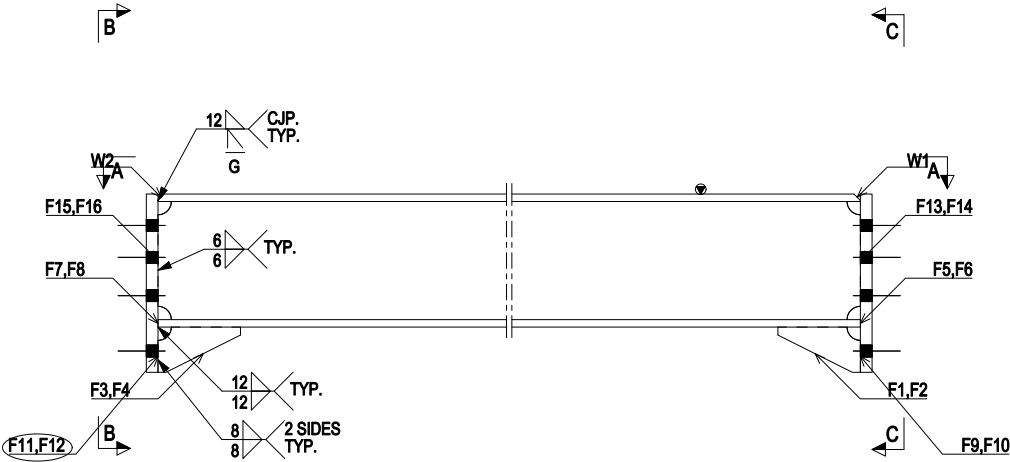

C - C
1:10

1 Beam BE021

1. ACCUMULATIVE DIMENSIONS ARE TAKEN FROM THE "TOP" LINE. 累积尺寸系从顶部线 "TOP" 开始计算。
2. ALL GAS RECOVERY COTS WILL HAVE A RADIUS OF 15mm UNLESS OTHERWISE SPECIFIED. 所有的气体回收罐除非另有规定，否则半径为 15mm。
3. ALL DIMENSIONS THIS SHEET TO BE PROVIDED Q355B-S-01. 本图的所有尺寸均需提供 Q355B-S-01。
4. ASSEMBLY MARK TO BE STAMPED ON THE FACE WHERE INDICATED THEREIN. 构件号打钢印，标记在图上。
5. "X" INDICATES THE TOUCH FACE OF MEMBERS, SHIP ALIEN SPOT THEREIN. "X" 表示接触面，船外点在此处。
6. ALL THE DIAMETER OF SCALLOP IS 25mm UNLESS OTHERWISE SPECIFIED. 所有圆角直径除非另有规定，均为 25mm。
7. ALL WELDS SHALL BE CONTINUOUS UNLESS OTHERWISE SPECIFIED. 所有焊缝必须是连续的，除非另有规定。
8. REAL WELDS OF 3MM FILLET WELD SHALL BE PROVIDED IN WELDED CONNECTIONS. 所有节点处的实际焊缝为 3mm 角焊缝。
9. TEMPORARY BOLTS SHALL BE RED COATED TO CORROSION FROM THE PERMANENT MOLT. 临时螺栓应涂红漆，以防永久腐蚀。

00	23JUN25	ISSUE FOR FABRICATION	WF	WW	YF	YF
REV	DATE	REVISION	BY	CHKD	APVD	APVD

RETURN TO VENDOR RESPOND BY

☐ 1 REVISE AND RESUBMIT

☐ 2 TO BE ISSUED AS FINAL PROVIDED COMMENTS ARE INCORPORATED

☐ 3 NOT COMMENT - FINAL ISSUE

☐ 4 FOR INFORMATION ONLY

North Field South Project
Onshore LNG Facilities

QatarEnergy LNG

THIS DOCUMENT IS PROPERTY OF QATARENERGY LTD. THIS DRAWING OR MATERIAL, DISCLOSED THEREIN MAY NOT BE COPIED OR REPRODUCED IN ANY FORM OR MANNER TO THIS FIRM, OR USED FOR OTHER THAN THE PROJECT FOR WHICH IT HAS BEEN PROVIDED, IN WHOLE OR IN PART, IN ANY MANNER EXCEPT AS EXPRESSLY PERMITTED BY QATARENERGY LTD.

COMPANY CONTRACT NO.:	LTCQNFBS649821	CONTRACTOR JOB NO.:	N/A
P.O.:	215777C008-00000-PO-1800-20301-NFS620		
REQUISITION NO.:	NFS_EPC-TECC-ST-REQ-20301		
EQUIPMENT NAME:	PACKAGE - III- STEEL STRUCTURES (Offshore Area)		
TAG NO.:	361-RC3210-S-01		
VENDOR NAME:	UNITED STEEL STRUCTURES LTD.		
DOCUMENT CLASS:	3		
VENDOR DOCUMENT NO.:	ST20301-02048		

TITLE INLET AREA STEEL STRUCTURE DRAWING 361-RC3210-S-01-BE021		SCALE 1:10	PROJECT NO. LTCQNFBS649821
PROJECT NFS	PROJECT DOCUMENT NO. 5496_21-ST20301-02045	SHEET No. 1	SIZE A3
			REVISION 00

1	A-B/1-2/QNHD +19.000
QTY	MEMBERS LOCATION