

Length 长度(mm)	Width 宽度(mm)	Height 高度(mm)
3937	692	338

Pay Cat. 付款等级	Line 行号	Qty. 数量
	1	1

Mark 构件号	Sub Mark 次构件号
BE019	

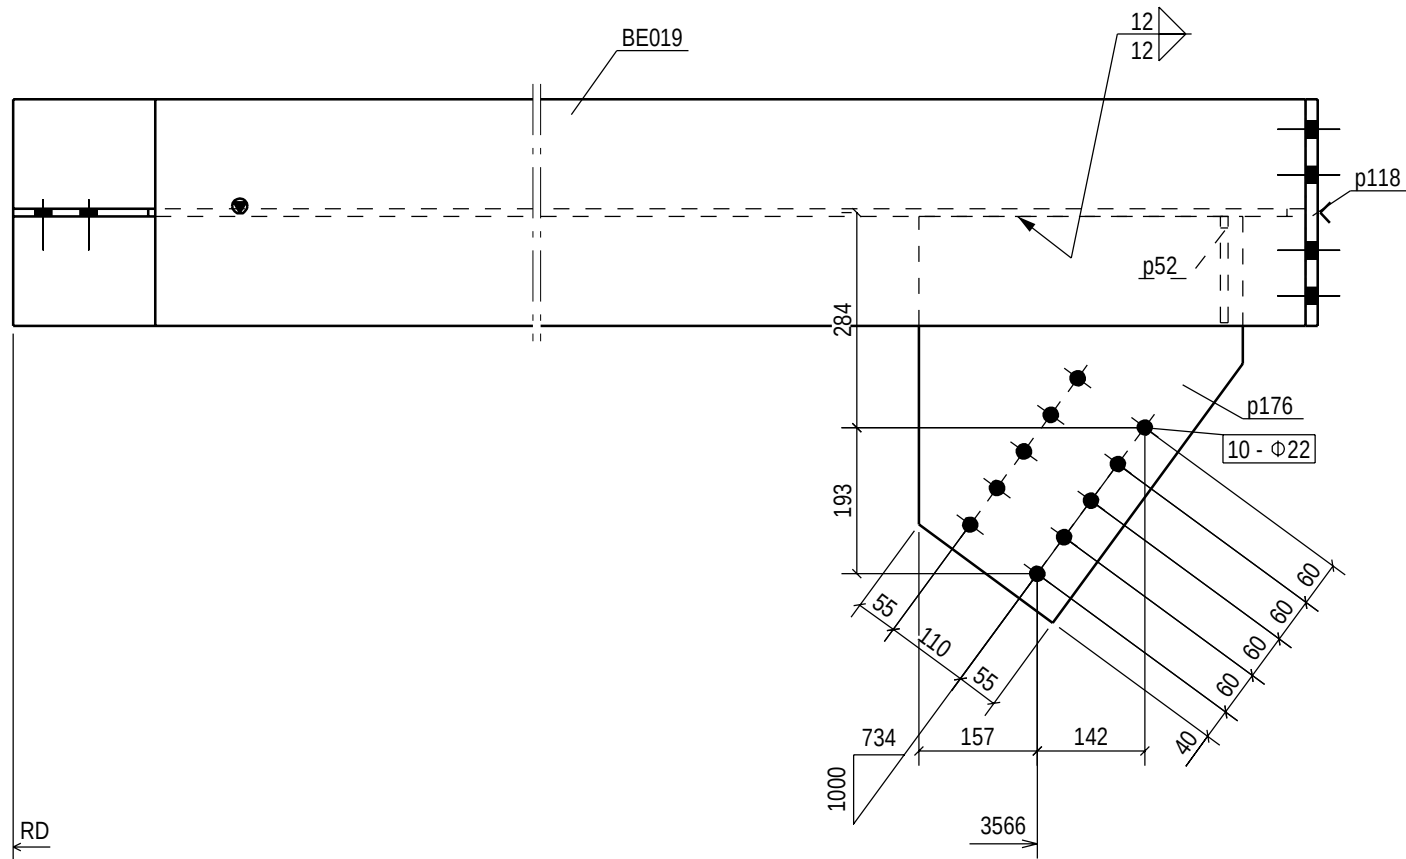
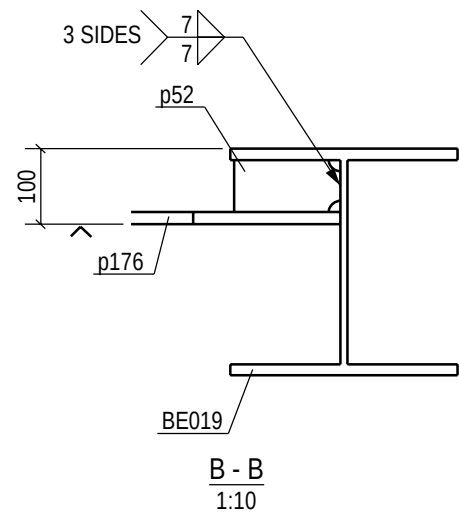
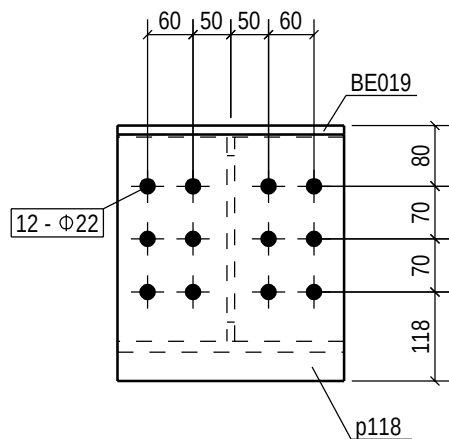
Description 截面尺寸	Material 材料
Beam	

Length 长度(mm)	Finish 油漆	ABM 材料订单号	Weight 重量(kg)	REMARK 备注

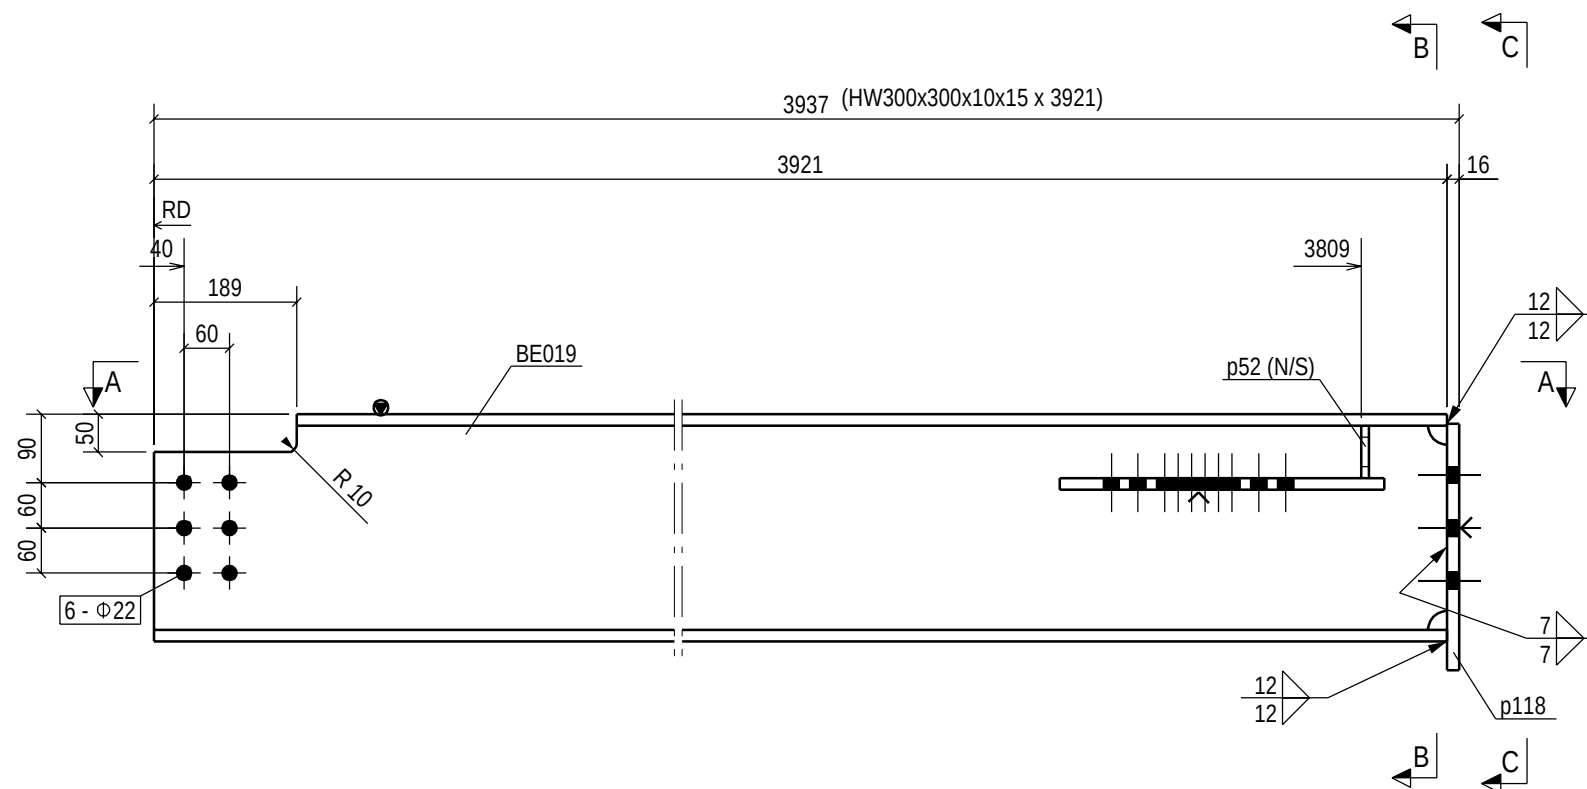
1810.02.10.03.12	2	1		BE019	HW300x300x10x15	Q355B	3921	G		357.65	
1810.02.10.03.12	3	1		p52	PL10x69	Q355B	140	G		0.73	
1810.02.10.03.12	4	1		p118	PL16x300	Q355B	326	G		12.28	
1810.02.10.03.12	5	1		p176	PL16x428.9	Q355B	537	G		22.08	
									TOTAL	382.74	

ASSEMBLY BOLT LIST (FOR 1 ASSEMBLY)						
Dia.	Grade	Pay Code	Length	No.	Site/Shop	
20	A325M	G	C1	55	6	Site

(Mechanical galvanized only for DTI washer)


$$\frac{A - A}{1:10}$$

$$\frac{B - B}{1:10}$$


C -
1:10



1	A-B/1-2/QNHD +17.200
QTY	MEMBERS LOCATION

1 Beam BE019

1. ACCUMULATIVE DIMENSIONS ARE TAKEN FROM THE "0" LINE 累积尺寸是从基准线"0"引出的尺寸
2. ALL GAS RE-ENTRANT OUTLETS HAVE A RADIUS OF 10mm 所有燃气回流出口均有10mm的圆角, 需另标注
3. ALL SUMMERS THIS SHEET TO BE PRE-FRIGED 此图所有三通接口都要预先预冷(361-RC2210-S-01)
4. ASSEMBLY MARK TO BE STAMPED ON THE FACE WHERE INDICATED THIS 零件号打在 标注上
5. "Y" DENOTES THE TOUCH FACE OF MEMBERS. SHOP MUST SPOT THEM. "Y"为两件的合面, Y 工厂标注位置
6. ALL THE DIAMETER OF SCALLOP IS 25mm U.O. 所有扇形圆角都是25mm, 需另标注
7. ALL WELDS SHALL BE CONTINUOUS U.O. 所有焊缝必须是连续焊, 需另标注
8. SEAL WELDS OF 3MM FILL WELD SHALL BE PROVIDED IN WELDED CONNECTIONS. 焊接节点的封焊是3mm的焊缝
9. TYPING BOOTS SHALL BE RED COATED TO DISTINGUISH FROM THE PERMANENT BOAT. 衬垫板靴要涂红漆, 以区别于永久板

00	23JUN25	ISSUE FOR FABRICATION	WFF ✱✱✱	WWF ✱ ✱ ✱	YF ✱✱✱	YF ✱✱✱	
REV	DATE	REVISION	BY	CHKD	APVD	APVD	

		PURCHASER'S PERMISSION TO PROCEED OR REVIEW TAKEN ON VENDOR PRINTS SHALL NOT RELIEVE VENDOR FROM ITS RESPONSIBILITY UNDER PURCHASE ORDER	
RETURN TO VENDOR		RESPOND BY	
☐	1. REVISE AND RESUBMIT		
☐	2. TO BE ISSUED AS FINAL PROVIDED COMMENTS ARE INCORPORATED		
☐	3. NOT COMMENT - FINAL ISSUE		
☐	4. FOR INFORMATION ONLY		

North Field South Project Onshore LNG Facilities



QatarEnergy LNG

THIS DOCUMENT IS PROPERTY OF QATARENERGY L.L.C. THIS DRAWING OR MATERIAL DESCRIBED THEREON MAY NOT BE COPIED OR DISCLOSED IN ANY FORM OR MEDIUM TO THIRD PARTIES, OR USED FOR OTHER THAN THE PURPOSE FOR WHICH IT HAS BEEN PROVIDED, IN WHOLE OR IN PART IN ANY MANNER EXCEPT AS EXPRESSLY PERMITTED BY QATARENERGY L.L.C.



COMPANY CONTRACT NO.:	LTCINF549621	CONTRACTOR JOB NO.:	N/A
P.O.:	215777C008-00000-PO-1800-20301-NF5520		
REQUISITION NO.:	NFS_EPC-TECC-ST-REQ-20301		
EQUIPMENT NAME:	PACKAGE - III- STEELSTRUCTURES (Offsite Area)		
TAG NO.:	361-RC3210-S-01		
VENDOR NAME:	UNITED STEEL STRUCTURES LTD.		
DOCUMENT CLASS:	3		
VENDOR DOCUMENT NO.:	ST20301-02048		

INLET AREA
STEEL STRUCTURE DRAWING
361-RC3210-S-01-BE019

SCALE 1:10		PROJECT NO. LTC/C/NFS/5496/21		
PROJECT NFS	PROJECT DOCUMENT NO. <u>5496_21-ST20301-02045</u>	SHEET No. 1	SIZE A2	REVISION 00