


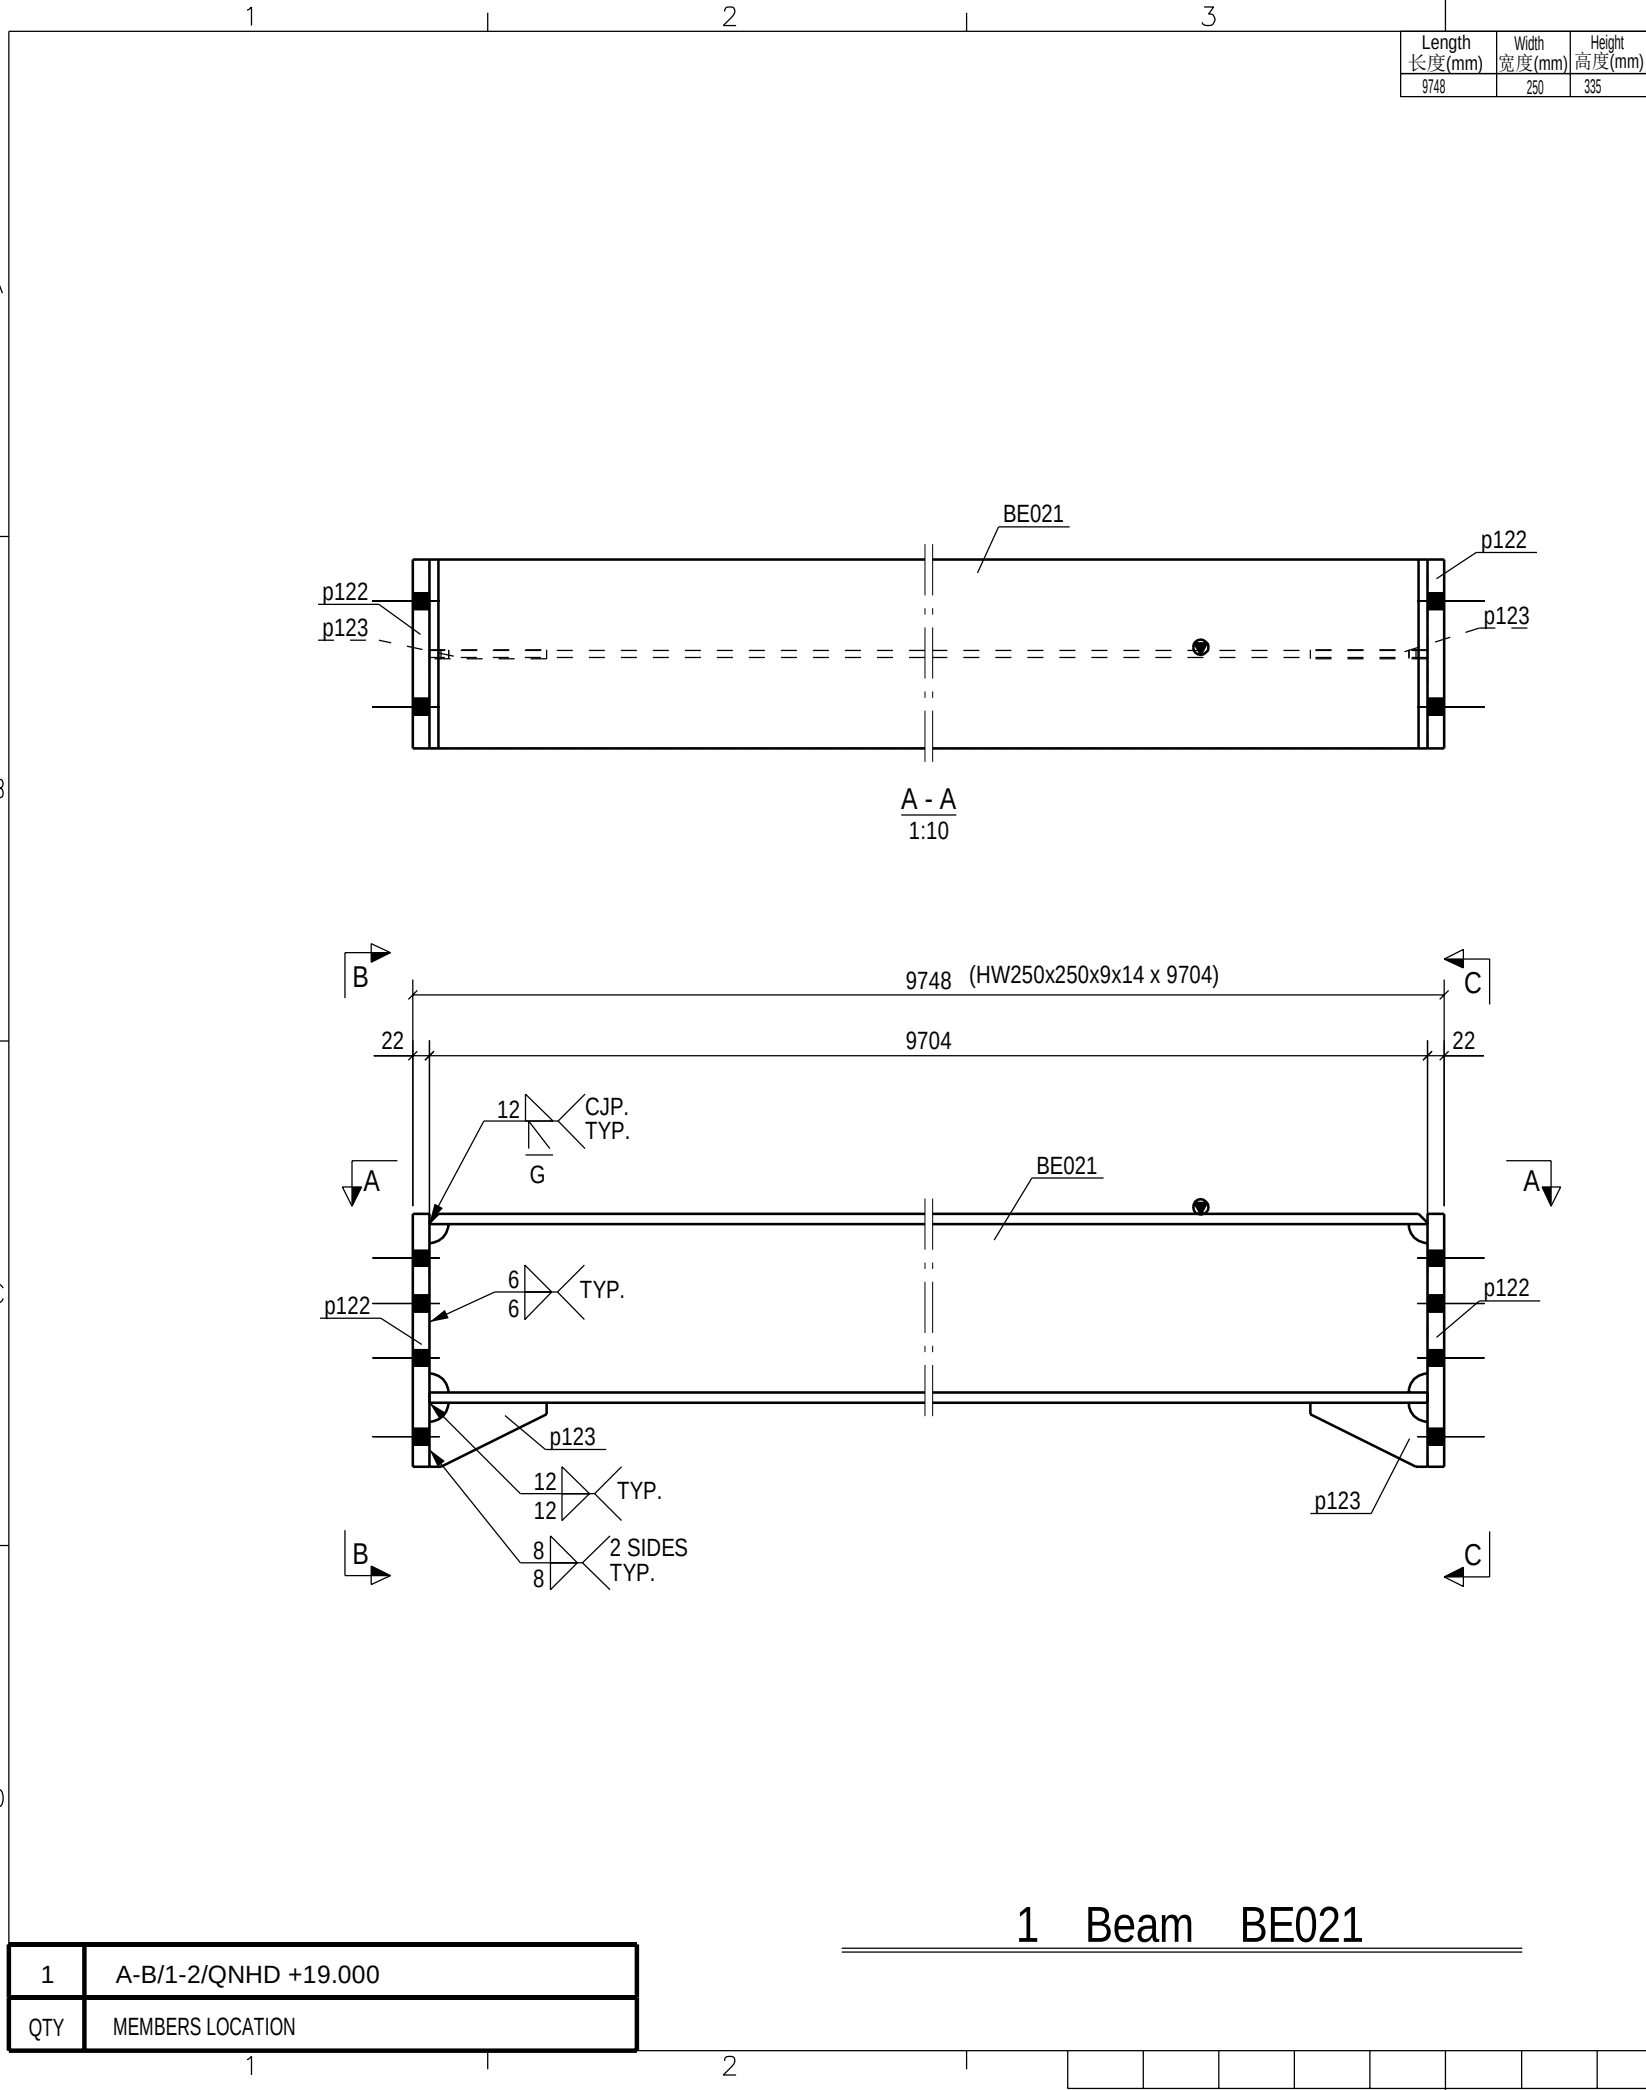

1. ACCUMULATIVE DIMENSIONS ARE TAKEN FROM THE "RO" LINE. 积累尺寸是根据该线"RO"开始计算。
2. ALL GAS RE-ENTRANT CUTS WILL HAVE A RADIUS OF 10mm U.N.O. 所有气割后切口要有10mm的半径, 除另有说明。
3. ALL SUBMARKS THIS SHEET TO BE PREFIXED (361-RC3210-S-01 这张图样的所有副标记前面要加 (361-RC3210-S-01
4. ASSEMBLY MARK TO BE STAMPED ON THE FACE WHERE INDICATED THUS 标记打在 标记面
5. ">" DENOTES THE TOUCH FACE OF MEMBERS. SHOP MUST SPOT THEM. ">" 为构件结合面, 工厂需标识出来。
6. ALL THE DIAMETER OF SCALLOP IS 25mm U.N.O. 所有圆形割角半径都是25mm, 除另有说明。
7. ALL WELDS SHALL BE CONTINUOUS. U.N.O. 所有焊缝都是连续焊缝, 除另有说明。
8. SEAL WELDS OF 3MM FILLET WELD SHALL BE PROVIDED IN WELDED CONNECTIONS. 焊接节点处的封焊是3mm角焊缝。
9. TEMPORARY BOLTS SHALL BE RED COATED TO DISTINGUISH FROM THE PERMANENT BOLT. 临时螺栓应涂红漆, 以区别于永久螺栓。

00	23JUN25	ISSUE FOR FABRICATION	WVF	WYW	YF	YF
REV	DATE	REVISION	BY	CHKD	APVD	APVD

T.EN CCC JV PURCHASER'S PERMISSION TO PROCEED OR REVIEW TAKEN ON VENDOR PRINTS SHALL NOT RELIEVE VENDOR FROM ITS RESPONSIBILITIES UNDER PURCHASE ORDER.

RETURN TO VENDOR RESPOND BY

☐ 1 REVISE AND RESUBMIT

☐ 2 TO BE ISSUED AS FINAL PROVIDED COMMENTS ARE INCORPORATED

☐ 3 NOT COMMENT - FINAL ISSUE

☐ 4 FOR INFORMATION ONLY

North Field South Project Onshore LNG Facilities

QatarEnergy LNG

THIS DOCUMENT IS PROPERTY OF QATARENERGY LNG. THIS DRAWING OR MATERIAL DESCRIBED THEREON MAY NOT BE COPIED OR DISCLOSED IN ANY FORM OR MEDIUM TO THIRD PARTIES, OR USED FOR OTHER THAN THE PURPOSE FOR WHICH IT HAS BEEN PROVIDED, IN WHOLE OR IN PART IN ANY MANNER EXCEPT AS EXPRESSLY PERMITTED BY QATARENERGY LNG.

United Steel Structures Ltd.

COMPANY CONTRACT NO.: LTC/CNFS/5496/21 CONTRACTOR JOB NO.: N/A

P.O.: 215777C008-00000-PO-1800-20301-NFS520

REQUISITION NO.: NFS_EPC-TECC-ST-REQ-20301

EQUIPMENT NAME: PACKAGE - III - STEEL STRUCTURES (Offsite Area)

TAG NO.: 361-RC3210-S-01

VENDOR NAME: UNITED STEEL STRUCTURES LTD.

DOCUMENT CLASS: 3

VENDOR DOCUMENT NO.: ST20301-02048

TITLE
INLET AREA
STEEL STRUCTURE DRAWING
361-RC3210-S-01-BE021

SCALE 1:10 PROJECT NO. LTC/CNFS/5496/21

PROJECT NFS PROJECT DOCUMENT NO. 5496_21-ST20301-02045 SHEET No. 1 SIZE A3 REVISION 00