


ASSEMBLY BOLT LIST (FOR 1 ASSEMBLY)						
Dia.	Grade		Pay Code	Length	No.	Site/Shop
20	A325M	G	C1	65	4	Site
20	A325M	G	C1	75	4	Site

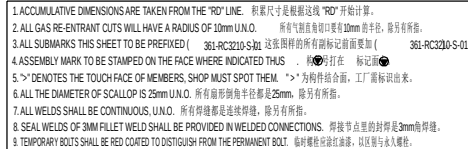

00	23JUN25	ISSUE FOR FABRICATION	WVF 문도복	WYW 유영우	YF 이현	YE 이현
REV	DATE	REVISION	BY	CHKD	APVD	APVD

		PURCHASER'S PERMISSION TO PROCEED OR REVIEW TAKEN ON VENDOR PRINTS SHALL NOT RELIEVE VENDOR FROM ITS RESPONSIBILITIES UNDER PURCHASE ORDER.	
RETURN TO VENDOR		RESPOND BY	
☐	1 REVISE AND RESUBMIT	_____	
☐	2 TO BE ISSUED AS FINAL PROVIDED COMMENTS ARE INCORPORATED	_____	
☐	3 NOT COMMENT - FINAL ISSUE	_____	
☐	4 FOR INFORMATION ONLY	_____	

North Field South Project Onshore LNG Facilities



QatarEnergy LNG

THIS DOCUMENT IS PROPERTY OF QATARENERGY LNG. THIS DRAWING OR MATERIAL DESCRIBED THEREON MAY NOT BE COPIED OR DISCLOSED IN ANY FORM OR MEDIUM TO THIRD PARTIES, OR USED FOR OTHER THAN THE PURPOSE FOR WHICH IT HAS BEEN PROVIDED, IN WHOLE OR IN PART IN ANY MANNER EXCEPT AS EXPRESSLY PERMITTED BY QATARENERGY LNG.



COMPANY CONTRACT NO.:	LTC/CNF5546621	CONTRACTOR JOB NO.:	N/A
P.O.:	215777C008-00000-PO-1800-20301-NFS520		
REQUISITION NO.:	NFS_EPC-TECC-ST-REQ-20301		
EQUIPMENT NAME:	PACKAGE - III- STEELSTRUCTURES (Offsite Area)		
TAG NO.:	361-RC3230-S-01		
VENDOR NAME:	UNITED STEEL STRUCTURES LTD.		
DOCUMENT CLASS:	3		
VENDOR DOCUMENT NO.:	ST20301-02048		

TITLE
INLET AREA
STEEL STRUCTURE DRAWING
361-RC3210-S-01-CO006

SCALE	1:10	PROJECT NO. LTC/C/NFS/5496/21			
PROJECT NFS	PROJECT DOCUMENT NO. <u>5496_21-ST20301-02045</u>	SHEET No. 1	SIZE A3	REVISION 	