

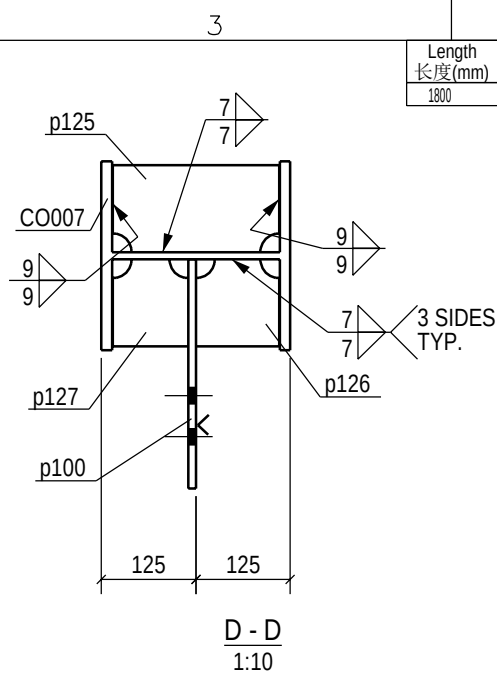


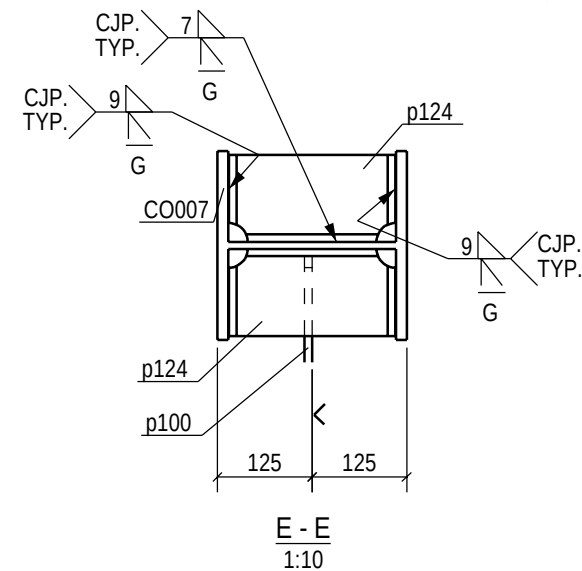

Pay Cat. 付款等级	Line 行号	Qty. 数量	Mark 构件号	Sub Mark 次构件号	Description 截面尺寸	Material 材质	Length 长度(mm)	Finish 油漆	ABM 材料订单号	Weight 重量(kg)	REMARK 备注
	1	1	CO007		Column						
1810.02.10.03.12	2	1		CO007	HW250x250x9x14	Q355B	1784	G		128.13	
1810.02.10.03.12	3	1		p47	PL16x290	Q355B	290	G		10.56	
1810.02.10.03.12	4	1		p100	PL10x312.7	Q355B	318	G		6.07	
1810.02.10.03.12	5	1		p101	PL10x115.5	Q355B	220	G		1.92	
1810.02.10.03.12	6	2		p124	PL12x115.5	Q355B	220	G		4.33	
1810.02.10.03.12	7	1		p125	PL12x115.5	Q355B	220	G		2.30	
1810.02.10.03.12	8	1		p126	PL12x110	Q355B	116	G		1.10	
1810.02.10.03.12	9	1		p127	PL12x100	Q355B	116	G		1.00	
									TOTAL	155.41	

(Mechanical galvanized only for DTI washer)

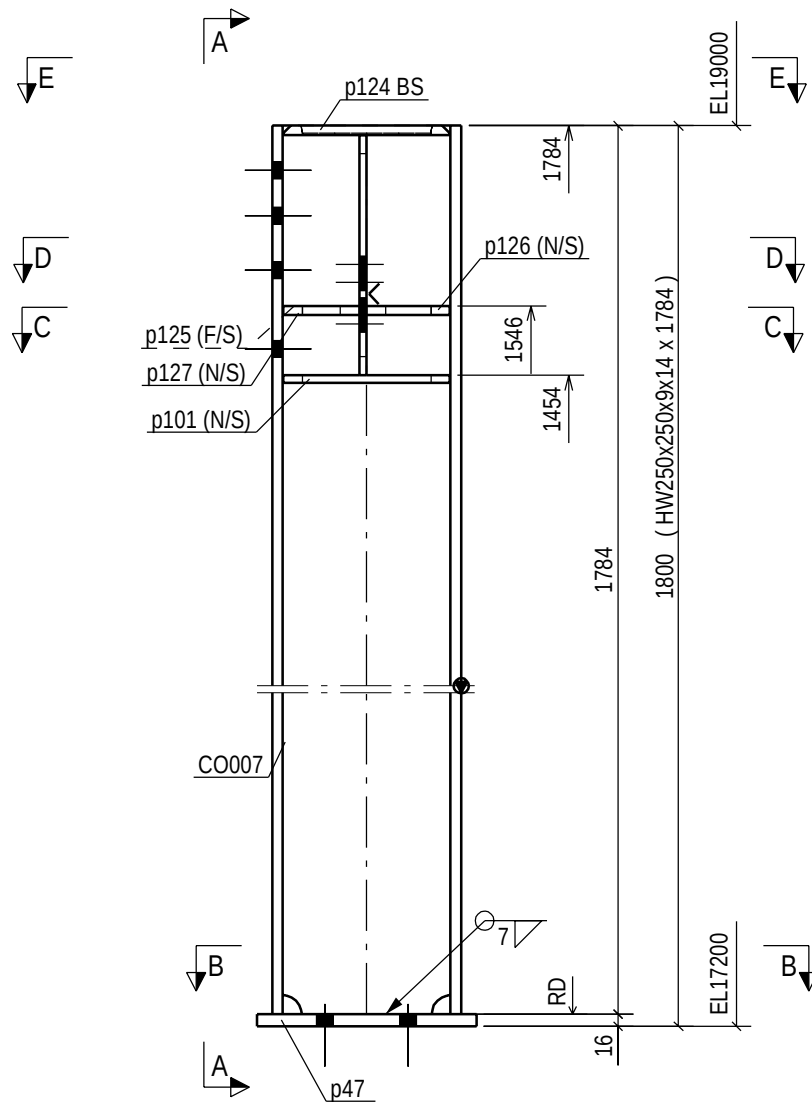

00	23JUN25	ISSUE FOR FABRICATION		WYF 張玉芳	WYW 劉永祥	YF 叶林	YF 叶林
REV	DATE	REVISION		BY	CHKD	APVD	APVD

		PURCHASER'S PERMISSION TO PROCEED OR REVIEW TAKEN ON VENDOR PRINTS SHALL NOT RELIEVE VENDOR FROM ITS RESPONSIBILITIES UNDER PURCHASE ORDER.	
RETURN TO VENDOR		RESPOND BY	
☐	1 REVISE AND RESUBMIT		
☐	2 TO BE ISSUED AS FINAL PROVIDED COMMENTS ARE INCORPORATED		
☐	3 NOT COMMENT - FINAL ISSUE		
☐	4 FOR INFORMATION ONLY		

North Field South Project Onshore LNG Facilities



QatarEnergy LNG

THIS DOCUMENT IS PROPERTY OF QATARENERGY LNG. THIS DRAWING OR MATERIAL DESCRIBED THEREON MAY NOT BE COPIED OR DISCLOSED IN ANY FORM OR MEDIUM TO THIRD PARTIES, OR USED FOR OTHER THAN THE PURPOSE FOR WHICH IT HAS BEEN PROVIDED, IN WHOLE OR IN PART IN ANY MANNER EXCEPT AS EXPRESSLY PERMITTED BY QATARENERGY LNG.



COMPANY CONTRACT NO.:	LTC/CNFS/5496/21	CONTRACTOR JOB NO.:	N/A
P.O.:	215777C008-00000-PO-1800-20301-NFS520		
REQUISITION NO.:	NFS_EPC-TECC-ST-REQ-20301		
EQUIPMENT NAME:	PACKAGE - III- STEELSTRUCTURES (Offsite Area)		
TAG NO.:	361-RC3210-S-01		
VENDOR NAME:	UNITED STEEL STRUCTURES LTD.		
DOCUMENT CLASS:	3		
VENDOR DOCUMENT NO.:	ST20301-02048		

TITLE
INLET AREA
STEEL STRUCTURE DRAWING
361-RC3210-S-01-CO007

SCALE 1:10		PROJECT NO. LTC/CNFS/5496/21		
PROJECT NFS	PROJECT DOCUMENT NO. 5496_21-ST20301-02045	SHEET No. 1	SIZE A3	REVISION 00

1. ACCUMULATIVE DIMENSIONS ARE TAKEN FROM THE "00" LINE 和尺寸累积是从第“00”开始计算。
2. ALL GAS RE-ENTRANT CUTS WILL HAVE A RADIUS OF 10MM 所有的气体回入切口将有10mm的半径。
3. ALL SUBMARKS THIS SHEET TO BE PREPARED (361, 8C2210 3-01) 这张图样的所有附页都要标注如 (361, 8C2210 3-01)
4. ASSEMBLY MARK TO BE STAMPED ON THE FACE WHERE INDICATED THIS 零件的打点 标记点
5. * DENOTES THE TOUCH FACE OF MEMBERS, SHOP MUST SPOT THEM. * 为接触面打点, 工厂必须打点。
6. ALL THE DIAMETER OF SCALP IS 25mm 所有面部的直径都是25mm, 除非有另图。
7. ALL WELDS SHALL BE CONTINUOUS, UNDO. 所有焊缝都是连续焊缝, 除非有另图。
8. SEAL WELDS OF 3MM FILLET WELD SHALL BE PROVIDED IN WELDED CONNECTIONS. 按设计点的焊缝是3mm的焊缝。
9. TEMPORARY BOLTS SHALL BE RED COATED TO DISTINGUISH FROM THE PERMANENT BOLTS. 临时螺栓要涂红漆, 以区分永久螺栓。

1	B/1-2/QNHD +19.000
QTY	MEMBERS LOCATION

1 Column CO007