


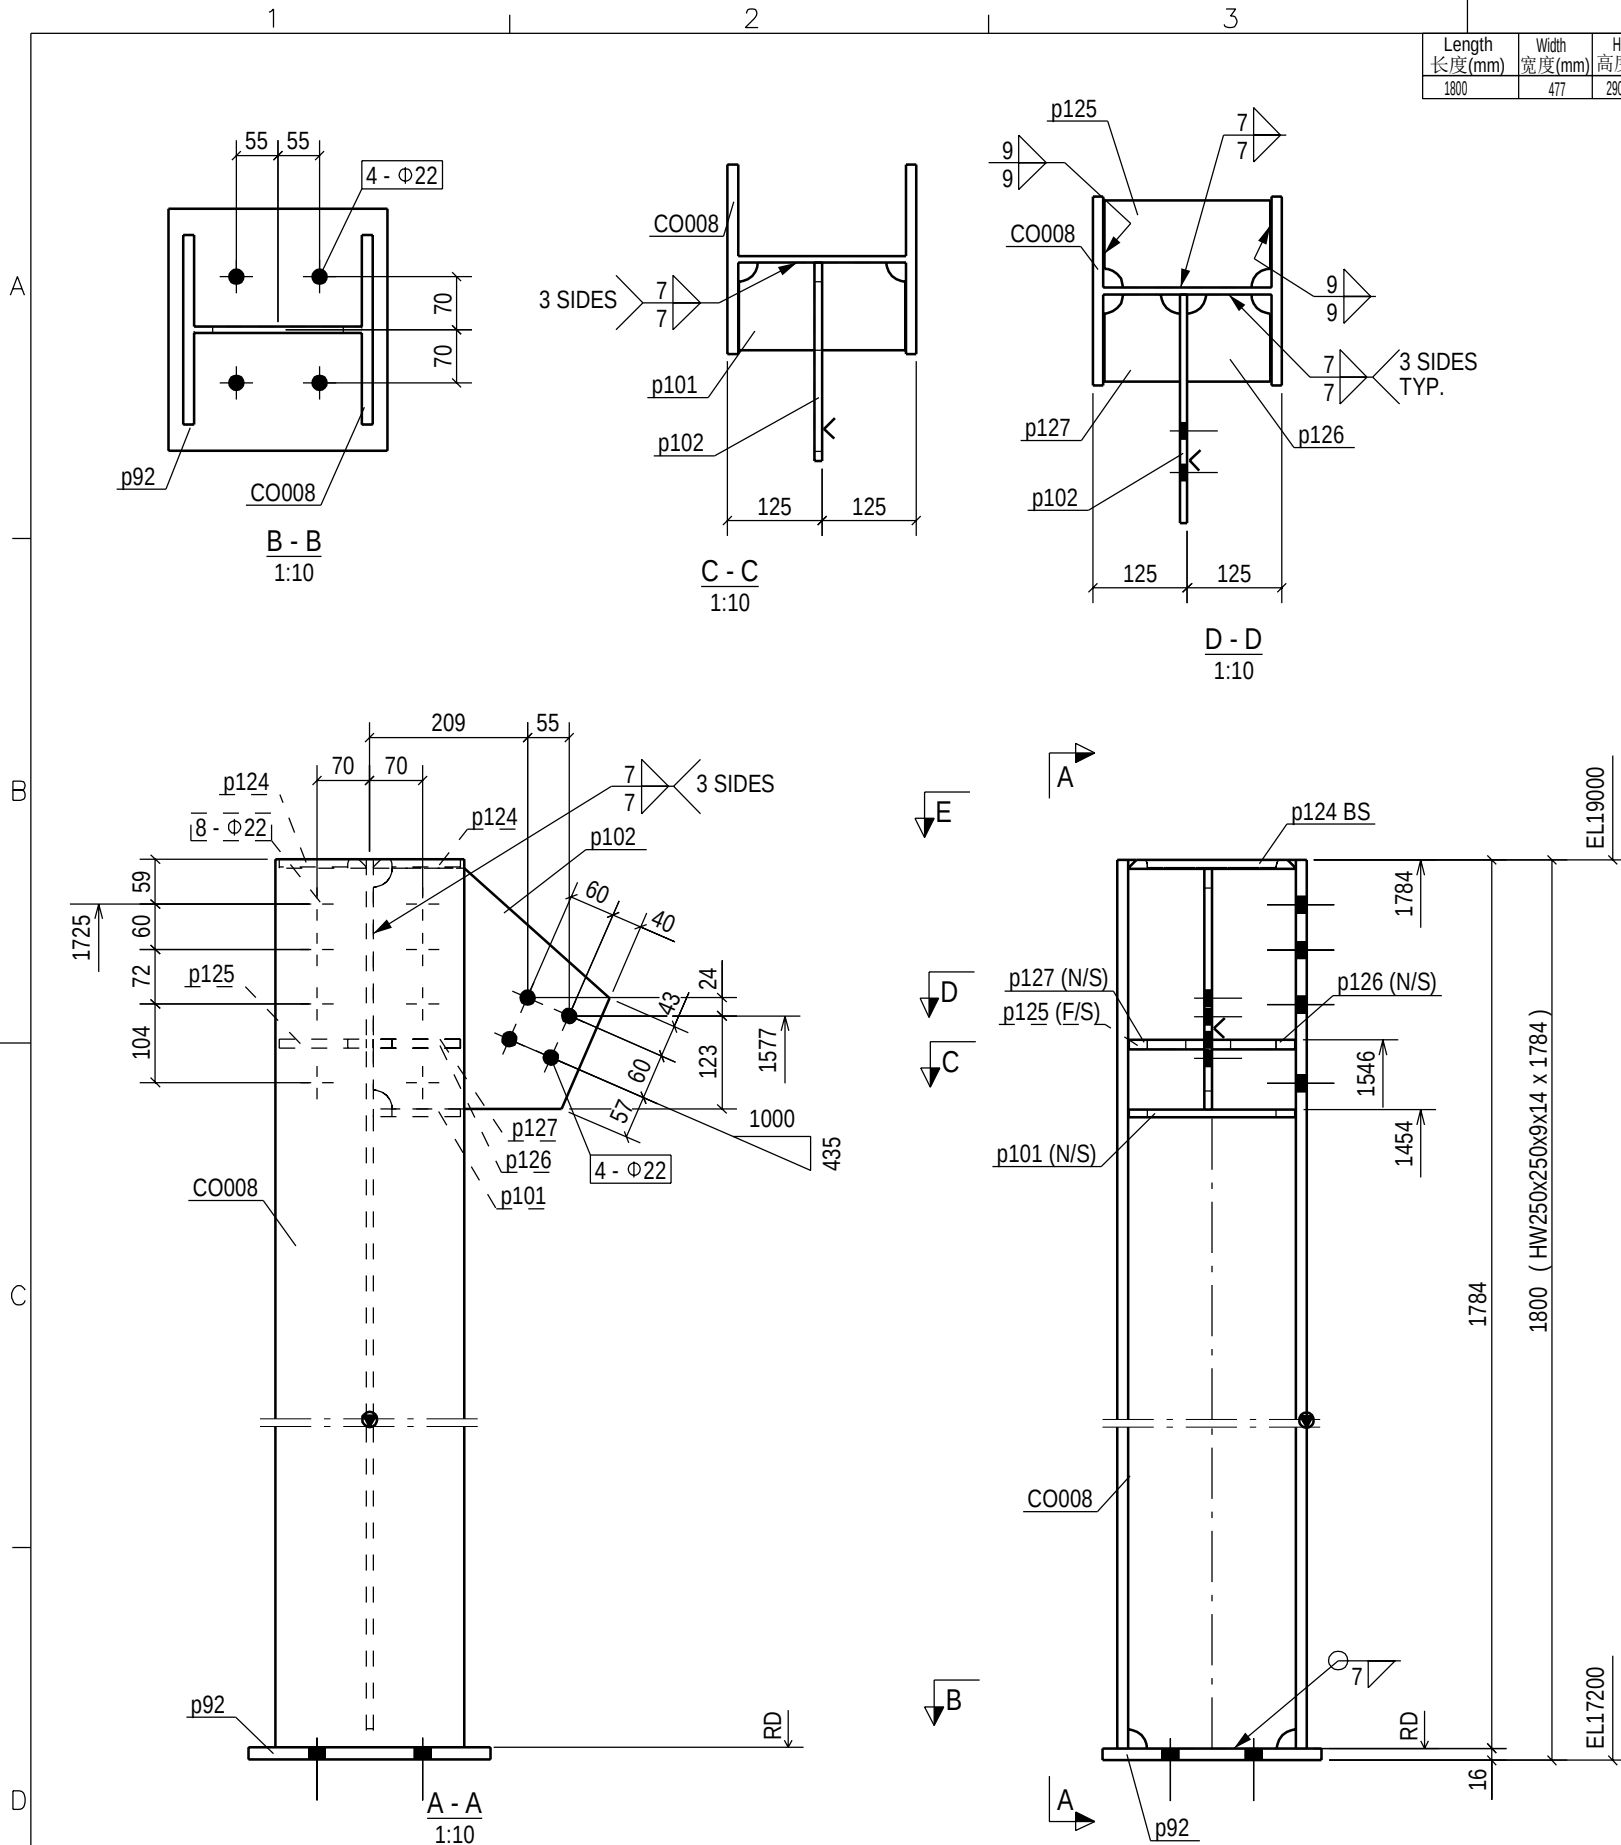

1	A/1-2/QNHD +19.000
QTY	MEMBERS LOCATION

1 Column CO008


Length 长度(mm)	Width 宽度(mm)	Height 高度(mm)
1800	477	290

Pay Cat. 付款等级	Line 行号	Qty. 数量	Mark 构件号	Sub Mark 次构件号	Description 截面尺寸	Material 材质	Length 长度(mm)	Finish 油漆	ABM 材料订单号	Weight 重量(kg)	REMARK 备注
	1	1	CO008		Column						
1810.02.10.03.12	2	1		CO008	HW250x250x9x14	Q355B	1784	G		128.13	
1810.02.10.03.12	3	1		p92	PL16x290	Q355B	320	G		11.66	
1810.02.10.03.12	4	1		p101	PL10x115.5	Q355B	220	G		1.92	
1810.02.10.03.12	5	1		p102	PL10x312.7	Q355B	318	G		6.07	
1810.02.10.03.12	6	2		p124	PL12x115.5	Q355B	220	G		4.33	
1810.02.10.03.12	7	1		p125	PL12x115.5	Q355B	220	G		2.30	
1810.02.10.03.12	8	1		p126	PL12x110	Q355B	116	G		1.10	
1810.02.10.03.12	9	1		p127	PL12x100	Q355B	116	G		1.00	
TOTAL										156.51	

ASSEMBLY BOLT LIST (FOR 1 ASSEMBLY)

Dia.	Grade		Pay Code	Length	No.	Site/Shop
20	A325M	G	C1	70	4	Site
20	A325M-DTI	G	C1	75	8	Site

(Mechanical galvanized only for DTI washer)

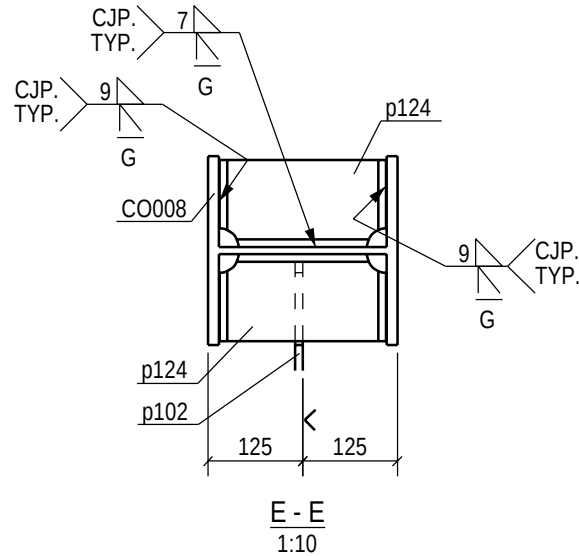

00	23JUN25	ISSUE FOR FABRICATION	WVF	WVW	YF	YF
REV	DATE	REVISION	BY	CHKD	APVD	APVD

PURCHASER'S PERMISSION TO PROCEED OR REVIEW TAKEN ON VENDOR PRINTS SHALL NOT RELIEVE VENDOR FROM ITS RESPONSIBILITIES UNDER PURCHASE ORDER.

RETURN TO VENDOR	RESPOND BY
☐ 1 REVISE AND RESUBMIT	
☐ 2 TO BE ISSUED AS FINAL PROVIDED COMMENTS ARE INCORPORATED	
☐ 3 NOT COMMENT - FINAL ISSUE	
☐ 4 FOR INFORMATION ONLY	

North Field South Project
Onshore LNG Facilities

QatarEnergy LNG
THIS DOCUMENT IS PROPERTY OF QATARENERGY LNG. THIS DRAWING OR MATERIAL DESCRIBED THEREON MAY NOT BE COPIED OR DISCLOSED IN ANY FORM OR MEDIUM TO THIRD PARTIES, OR USED FOR OTHER THAN THE PURPOSE FOR WHICH IT HAS BEEN PROVIDED, IN WHOLE OR IN PART IN ANY MANNER EXCEPT AS EXPRESSLY PERMITTED BY QATARENERGY LNG.



COMPANY CONTRACT NO.:	LTC/INF/S496/21	CONTRACTOR JOB NO.:	N/A
P.O.:	215777C008-00000-PO-1800-20301-NFS520		
REQUISITION NO.:	NFS_EPC-TECC-ST-REQ-20301		
EQUIPMENT NAME:	PACKAGE - III - STEEL STRUCTURES (Offsite Area)		
TAG NO.:	361-RC3210-S-01		
VENDOR NAME:	UNITED STEEL STRUCTURES LTD.		
DOCUMENT CLASS:	3		
VENDOR DOCUMENT NO.:	ST20301-02048		

TITLE
INLET AREA
STEEL STRUCTURE DRAWING
361-RC3210-S-01-CO008

SCALE	1:10	PROJECT NO.	LTC/CNFS/5496/21
PROJECT	NFS	PROJECT DOCUMENT NO.	5496_21-ST20301-02045
SHEET No.	1	SIZE	A3
REVISION	00		

1. ACCUMULATIVE DIMENSIONS ARE TAKEN FROM THE "RD" LINE. 积累尺寸是根据该线"RD"开始计算。
2. ALL GAS RE-ENTRANT CUTS WILL HAVE A RADIUS OF 10mm U.N.O. 所有气侧直管切口要有10mm的半径, 除另有说明。
3. ALL SUBMARKS THIS SHEET TO BE PREFIXED (361-RC3210-S-01 在这张图样的所有标注前面增加 361-RC3210-S-01
4. ASSEMBLY MARK TO BE STAMPED ON THE FACE WHERE INDICATED THUS 标注打在 标记面
5. ">" DENOTES THE TOUCH FACE OF MEMBERS. SHOP MUST SPOT THEM. ">" 为构件结合面, 工厂需标识出来。
6. ALL THE DIAMETER OF SCALLOP IS 25mm U.N.O. 所有圆形割角半径都是25mm, 除另有说明。
7. ALL WELDS SHALL BE CONTINUOUS, U.N.O. 所有焊缝都是连续焊缝, 除另有说明。
8. SEAL WELDS OF 3MM FILLET WELD SHALL BE PROVIDED IN WELDED CONNECTIONS. 焊接节点处的封焊是3mm角焊缝。
9. TEMPORARY BOLTS SHALL BE RED COATED TO DISTINGUISH FROM THE PERMANENT BOLT. 临时螺栓应涂红漆, 以区别于永久螺栓。