

A
B
C
D
E
F

1

2

3

4

5







6

7

8

Length 长度(mm)	Width 宽度(mm)	Height 高度(mm)	Pay Cat. 付款等级	Line 行号	Qty. 数量	Mark 构件号	Sub Mark 次构件号	Description 截面尺寸	Material 材质	Length 长度(mm)	Finish 油漆	ABM 材料订单号	Weight 重量(kg)	REMARK 备注
5375	450	827		1	2	CO009		Column						
1810.02.10.05.12				2	2		CO009	HW414x405x18x28	Q355B	5175	G		2402.71	
1810.02.10.05.12				3	2		p7	PL50x450	Q355B	450	G		158.96	
1810.02.10.05.12				4	4		p15	PL25x150	Q355B	188	G		21.53	
1810.02.10.05.12				5	2		p16	PL25x150	Q355B	400	G		23.55	
1810.02.10.05.12				6	2		p17	PL12x38	Q355B	70	G		0.50	
1810.02.10.05.12				7	2		p143	PL16x342.9	Q355B	604	G		29.18	
1810.02.10.05.12				8	4		p144	PL10x189.5	Q355B	222	G		12.96	
1810.02.10.05.12				9	8		sp20	PL14x90	Q355B	90	G		7.12	
				10	8			24 ØA307 Shipping bolt / Nut		95				
												TOTAL	2656.52	

ASSEMBLY BOLT LIST (FOR 1 ASSEMBLY)					
Dia.	Grade	Pay Code	Length	No.	Site/Shop
(Mechanical galvanized only for DT1 washer)					

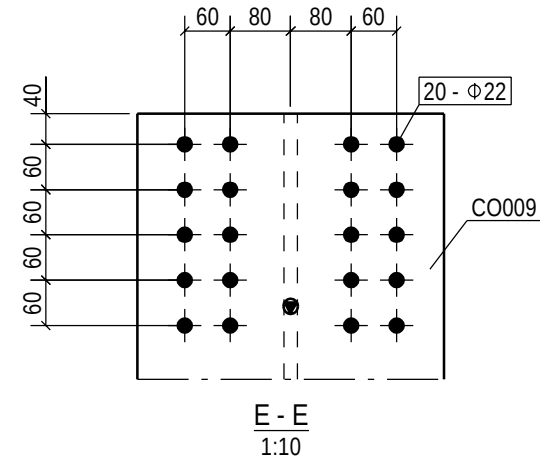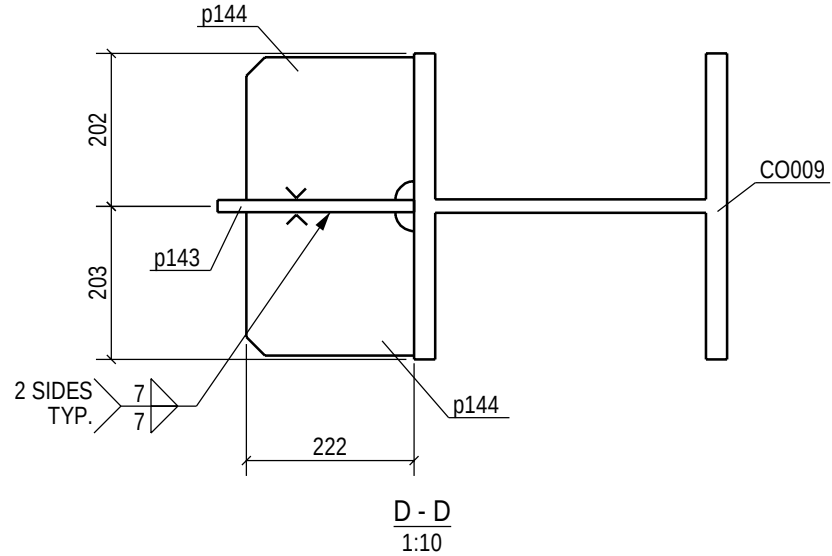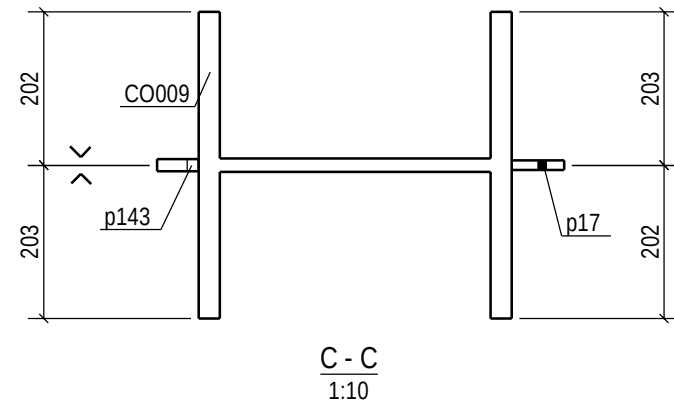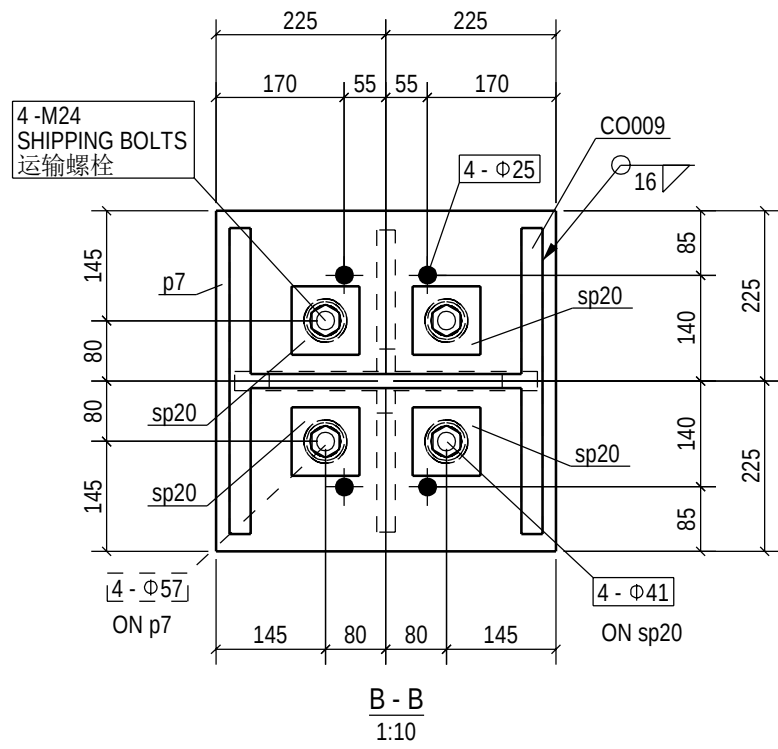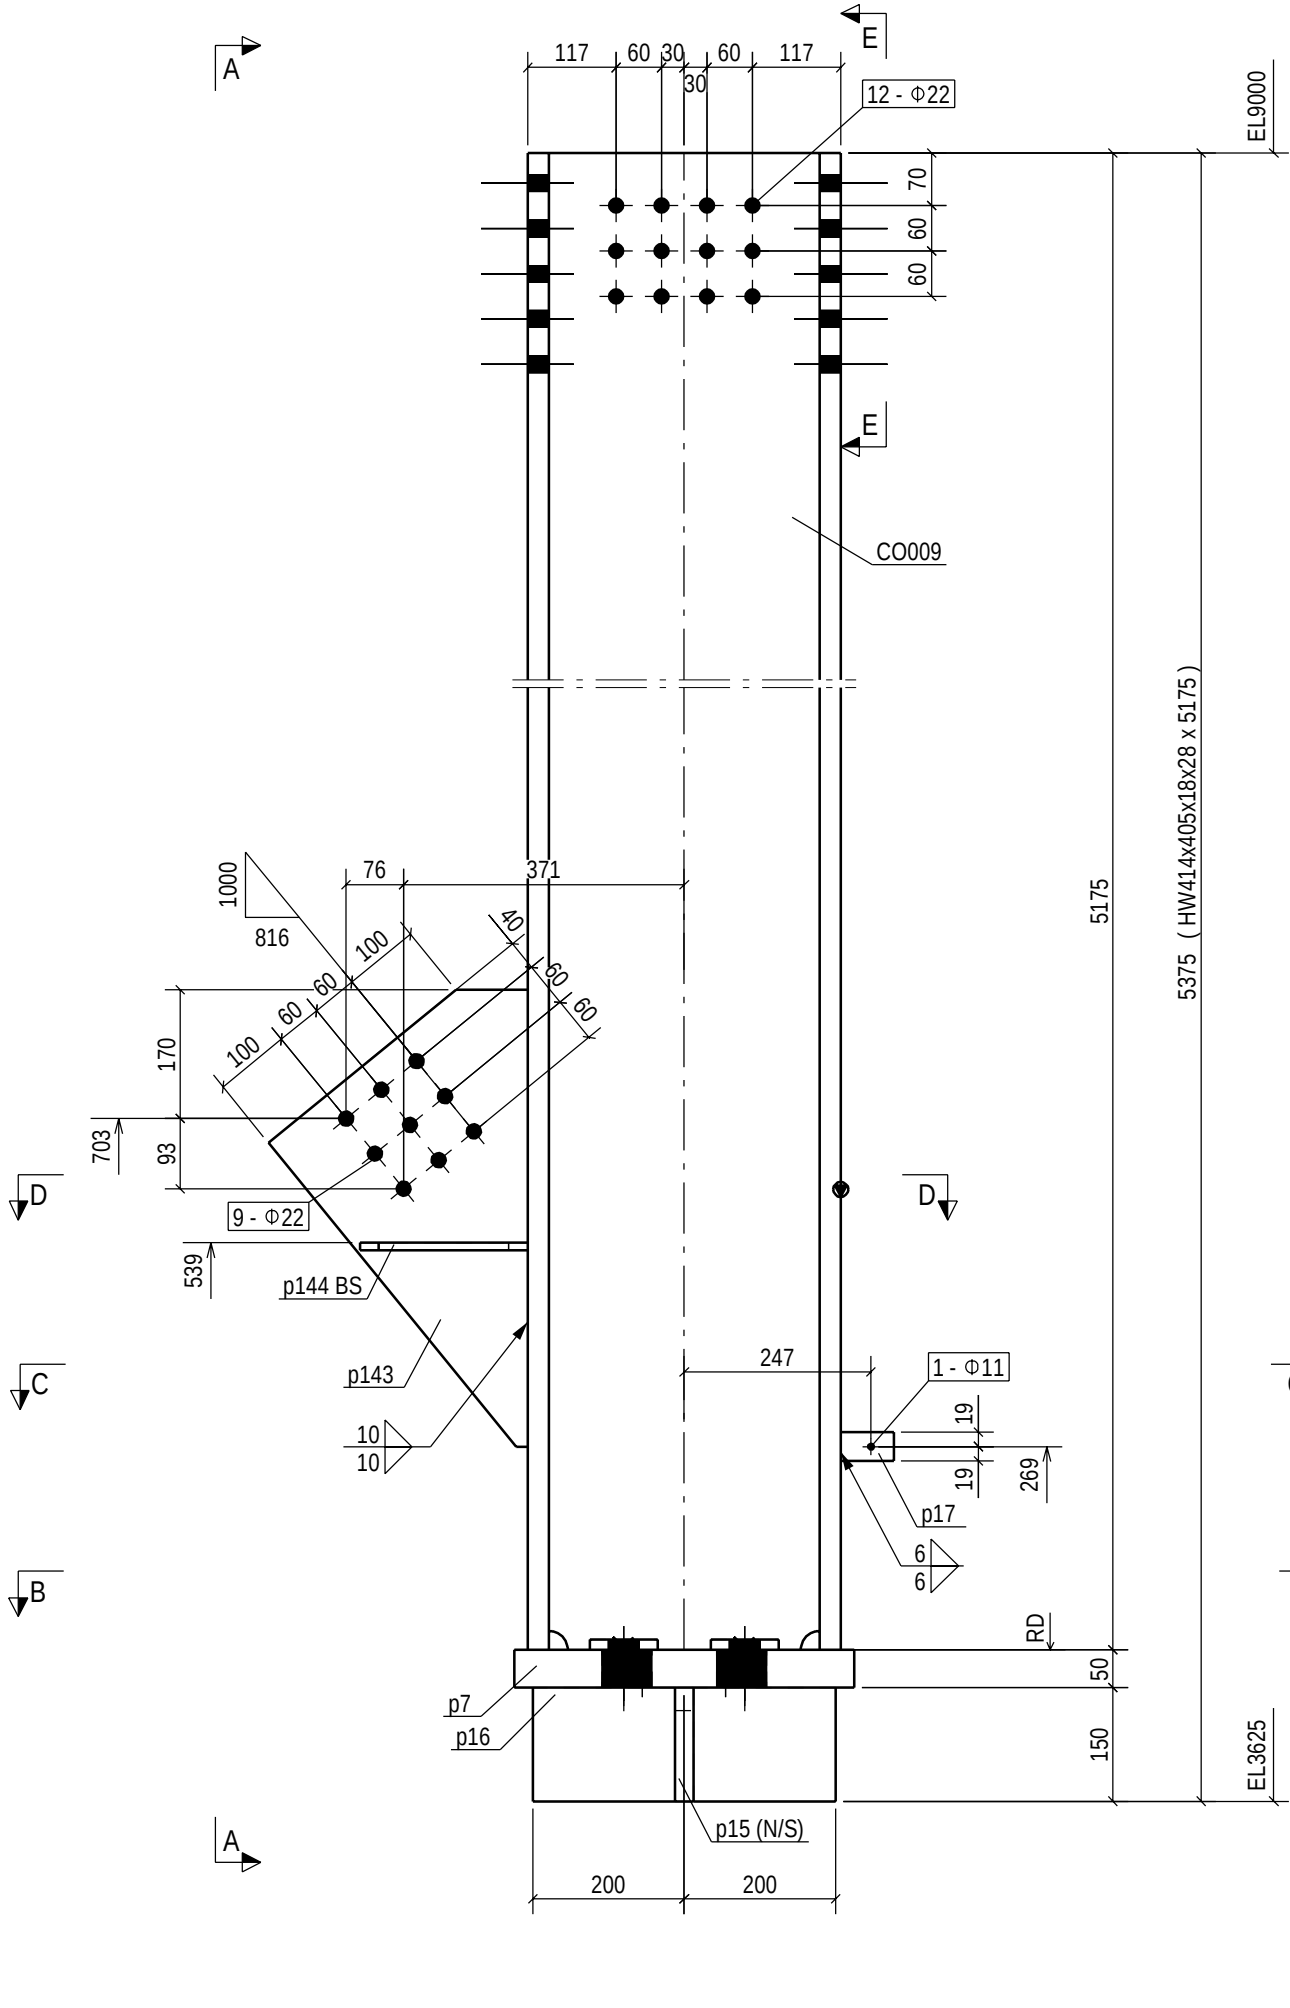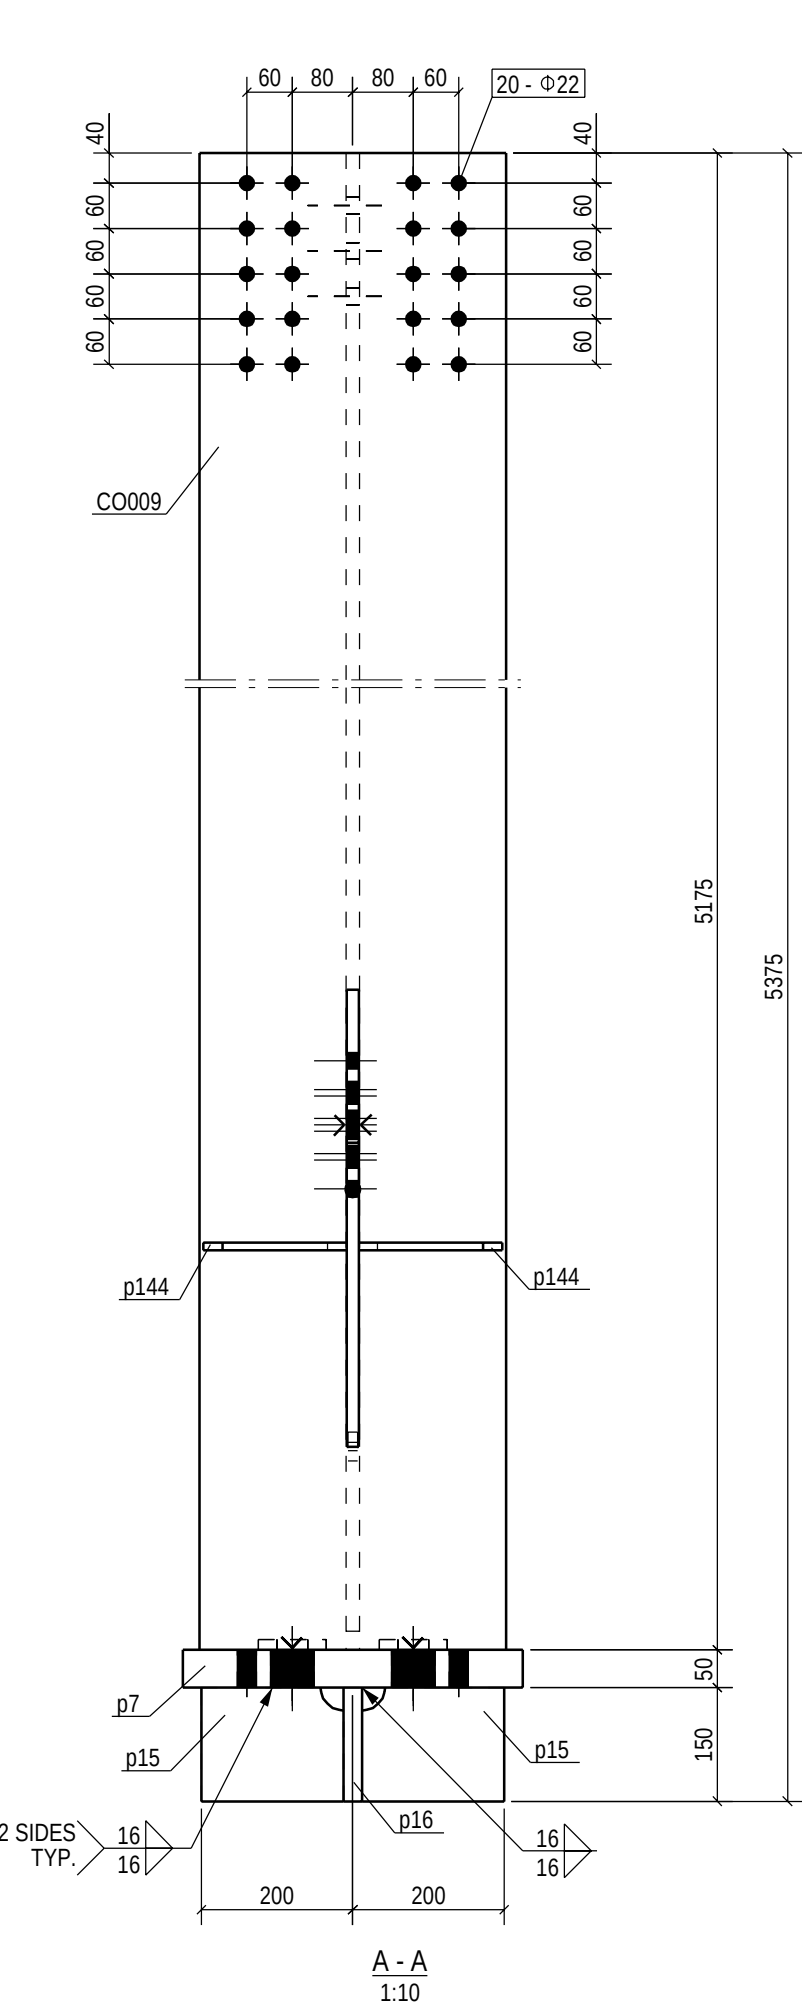

1	B/1/QNHD +9.000
1	A/1/QNHD +9.000
QTY	MEMBERS LOCATION

2 Columns CO009

1. ACCUMULATIVE DIMENSIONS ARE TAKEN FROM THE "R0" LINE. 累积尺寸是根据该 "R0" 线设计的。
2. ALL GAS RE-ENTRANT CUTS WILL HAVE A RADIUS OF 3mm UNLESS OTHERWISE SPECIFIED. 除非另有说明, 所有气体回流切口必须有 3mm 圆角。
3. ALL SUBMARKS THIS SHEET TO BE PREPARED BY 361-RC3210-S-01. 此图的所有标注均由 361-RC3210-S-01 准备。
4. ASSEMBLY MARK TO BE STAMPED ON THE FACE WHERE INDICATED THUS: 零件号打表 在 1 处。 361-RC3210-S-01
5. "Y" DENOTES THE TOUCH FACE OF MEMBERS. SHOP MUST SPOT THEM. "Y" 为构件接触面, 工厂需标注。
6. ALL THE DIAMETER OF SCALLOP IS 25mm UNLESS OTHERWISE SPECIFIED. 除非另有说明, 所有圆角切口直径均为 25mm。
7. ALL WELDS SHALL BE CONTINUOUS UNLESS OTHERWISE SPECIFIED. 除非另有说明, 所有焊缝必须是连续的。
8. SEAL WELDS OF 3MM FILLET WELD SHALL BE PROVIDED IN WELDED CONNECTIONS. 焊缝节点处应提供 3mm 密封焊。
9. TEMPORARY BOLTS SHALL BE RED COATED TO DISTINGUISH FROM THE PERMANENT BOLT. 临时螺栓应涂红色, 以区别于永久螺栓。

00	23JUN25	ISSUE FOR FABRICATION	WTF	WW	YF	YF
REV	DATE	REVISION	BY	CHKD	APVD	APVD
TEN CCC JV			PURCHASER'S PERMISSION TO PROCEED OR REVIEW TAKEN ON VENDOR PRINTS SHALL NOT RELIEVE VENDOR FROM ITS RESPONSIBILITIES UNDER PURCHASE ORDER.			
RETURN TO VENDOR			RESPOND BY			
☐ 1. REVISE AND RESUBMIT						
☐ 2. TO BE ISSUED AS FINAL PROVIDED COMMENTS ARE INCORPORATED						
☐ 3. NOT COMMENT - FINAL ISSUE						
☐ 4. FOR INFORMATION ONLY						
North Field South Project Onshore LNG Facilities						
QatarEnergy LNG			THIS DOCUMENT IS PROPERTY OF QATAR ENERGY LNG. THIS DRAWING OR MATERIAL DESCRIBED THEREIN MAY NOT BE COPIED OR DISCLOSED IN ANY FORM OR MEDIUM TO THIRD PARTIES OR USED FOR ANY OTHER PURPOSE WITHOUT THE EXPRESS WRITTEN PERMISSION OF QATAR ENERGY LNG.			
COMPANY CONTRACT NO.: LTC/CNFS/5496/21			CONTRACTOR JOB NO.: N/A			
P.O.: 215777C008-00000-PO-1800-20301-NFSS20						
REQUISITION NO.: NFS_EPC-TECC-ST-REQ-20301						
EQUIPMENT NAME: PACKAGE - III- STEELSTRUCTURES (Offsite Area)						
TAG NO.: 361-RC3210-S-01						
VENDOR NAME: UNITED STEEL STRUCTURES LTD.						
DOCUMENT CLASS: 3						
VENDOR DOCUMENT NO.: ST20301-02048						
TITLE INLET AREA STEEL STRUCTURE DRAWING 361-RC3210-S-01-CO009						
SCALE: 1:10		PROJECT NO: LTC/CNFS/5496/21				
PROJECT: NFS	PROJECT DOCUMENT NO: 5496_21-ST20301-02045	SHEET No: 1	SIZE: A2	REVISION: 00		