


Part list for one assembly marked: AC0003										Q.ty tot.
TCM Finish.1 Code: Fireproof										Q.ty tot.
TCM Finish.1 Code: Fireproof										Q.ty tot.
Part.N.	Q.ty	Profile	Material	Length [mm]	Weight [kg]		Area [m ²]			
					Unit	Total	Unit	Total		
A0008	2	UPN100	S355J2	805	8.53	17.06	0.30	0.60		
A0101	2	UPN120	S355J2	1055	14.08	28.16	0.46	0.92		
A0200	1	PL12*230	S355J2+Z15	220	4.77	4.77	0.1	0.1		
AC0003	1	HEA200	S355J2	836	35.41	35.41	0.95	0.95		
Assembly total										2.58

FINISHING SPECIFICATION					
	Substrate	Surface Preparation and Blast Profile	3	Generic System Details	DFT (µm)
PAINTING CYCLE	CS	ISO 8501-1 grade Sa 2.5 or SSPC-SP 10	1.2	A Epoxy / ESI	80-100
				B Polyurethane	100-80
				System NDFT (µm)	180
FINISH COAT COLOR					

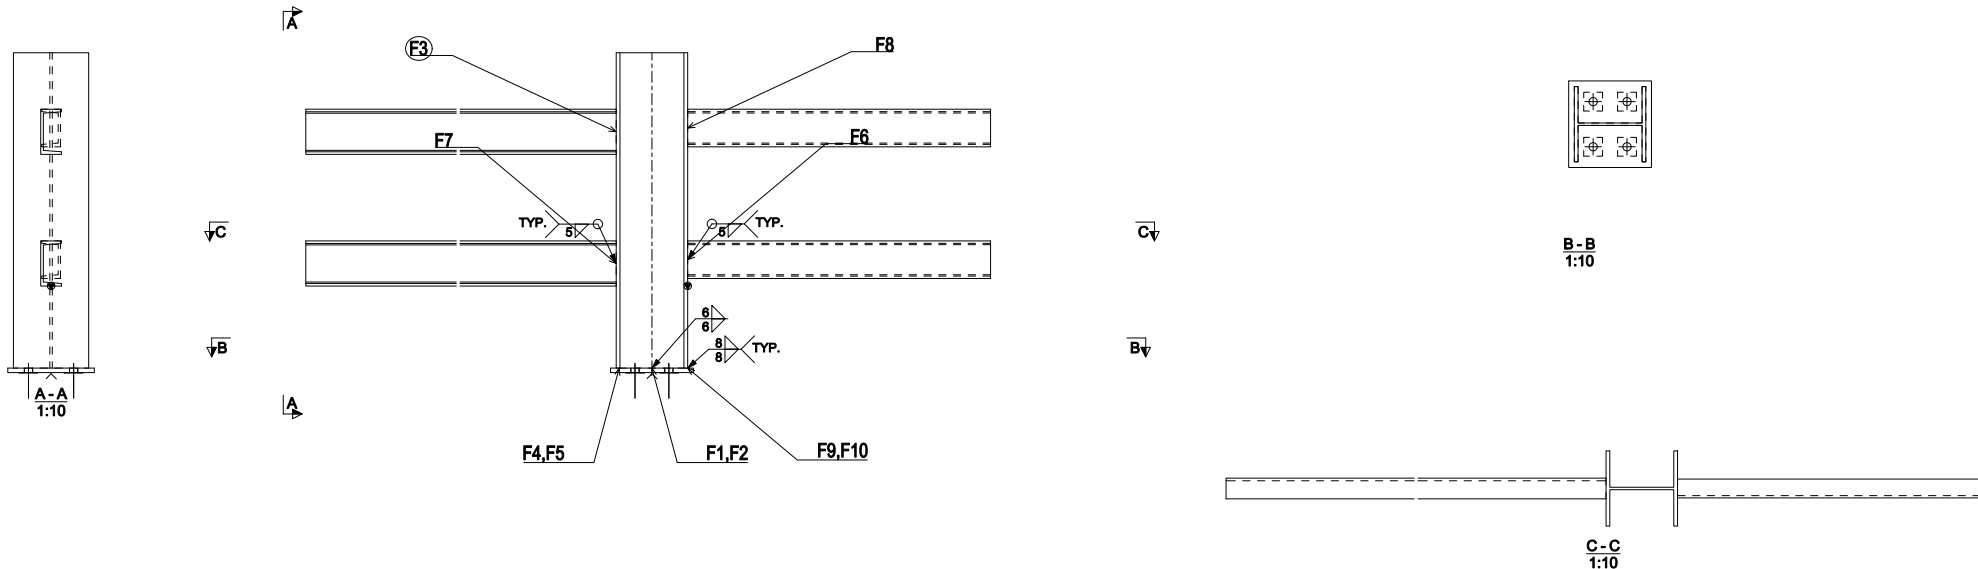

00	04.02.2026	ISSUED FOR CONSTRUCTION	Z.Neng	X.Qiang	Z.YingDong
REV.	DATE	REASON FOR ISSUE	PREPARED	CHECKED	APPROVED
   			MANUFACTURER 		
			VENDOR DRAWING No. AC0003		
			DOC. CLASS: 03		
PROJECT TITLE			SILLEN EPC PE UNITS, LAO AND UI&O		
DRAWING TITLE			INTERCONNECTING PIPE RACK (IPR) SECTION 1 SHOP DRAWING OF COLUMN 8901IR004I01AC0003		
SHEET SIZE A2		PURCHASE ORDER NUMBER 7500137917			REVISION 00
SCALE: 1:10		MATERIAL REQUISITION NUMBER 001T01			SHEET 1 of 1

GENERAL NOTES

- Steel structure fabrication shall comply with the requirements of last issue of 4503-AI-DX-T0000001
- Unless otherwise specified, fillet welds shall be as per following scheme:

- Where required, masking area shall be provided on contact surface sides. Unless otherwise specified, masking size and pattern according to below mask details for painting: