
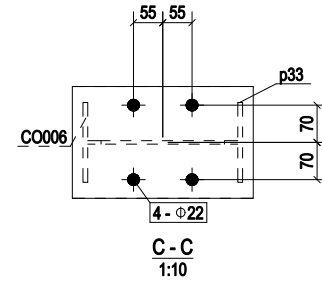
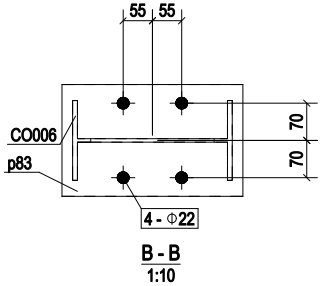


Length 长度(mm)	Width 宽度(mm)	Height 高度(mm)	Pay Cat. 付款等级	Line 行号	Qty 数量	Mark 构件号	Sub Mark 次构件号	Description 描述尺寸	Material 材质	Length 长度(mm)	Finish 油漆	ABM 材料订单号	Weight 重量(kg)	REMARK 备注
2998	210	340		1	1	CO006		Column						
1810.02.10.02.12				2	1		CO006	HN300x150x6.5x8	Q355B	2958	G		108.78	
1810.02.10.02.12				3	1		p33	PL20x210	Q355B	340	G		11.21	
1810.02.10.02.12				4	1		p83	PL20x210	Q355B	340	G		11.21	
												TOTAL	131.20	

ASSEMBLY BOLT LIST (FOR 1 ASSEMBLY)

Dia.	Grade		Pay Code	Length	No.	Site/Shop
20	A325M	G	C1	65	4	Site
20	A325M	G	C1	75	4	Site

(Mechanical galvanized only for DTI washer)

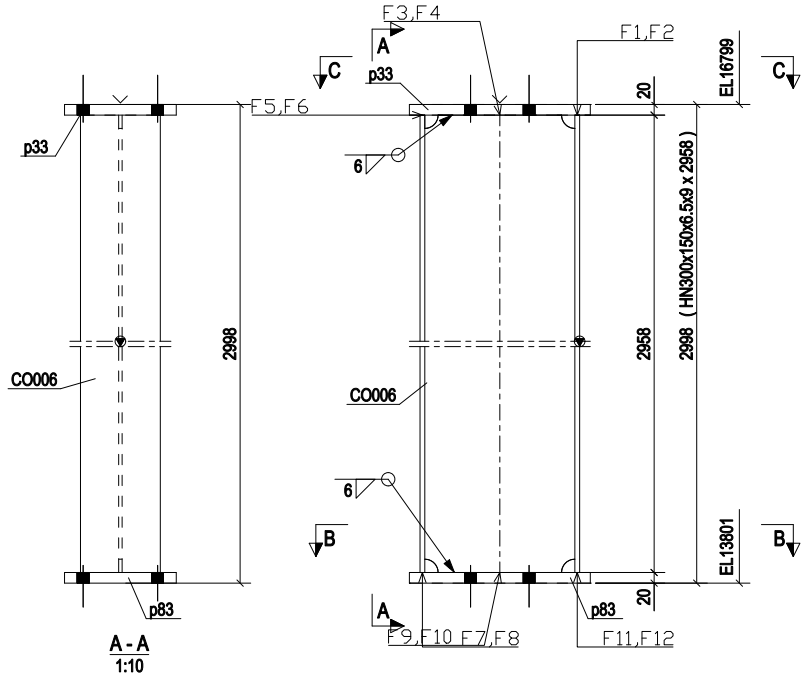

1 Column CO006

1	A/1-2/QNHD +16.799
QTY	MEMBERS LOCATION

1. ACCUMULATIVE DIMENSIONS ARE TAKEN FROM THE "TOP" LINE. 累积尺寸系从顶部线 "TOP" 开始计算。
2. ALL GAS RECOVERY COTS WILL HAVE A RADIUS OF 15mm UNLESS NOTED. 所有气体回收罐除非另有说明，均为15mm半径。
3. ALL DIMENSIONS THIS SHEET TO BE PRECEDED QJ-RC3210-S-01. 本图所有尺寸均须以 QJ-RC3210-S-01 为前缀。
4. ASSEMBLY MARK TO BE STAMPED ON THE FACE WHERE INDICATED THEREIN. 构件号打钢印，标注在图上。
5. "P" INDICATES THE TOUCH FACE OF MEMBERS, SHIP ALIGHT SPOT THERE. "P" 为构件接触面，2T 船岸对接点。
6. ALL THE DIAMETER OF SCALLOP IS 25mm UNLESS NOTED. 所有圆角半径除非另有说明，均为25mm。
7. ALL WELDS SHALL BE CONTINUOUS UNLESS NOTED. 所有焊缝必须是连续焊缝，除非另有说明。
8. REAL WELDS OF 3MM FILLET WELD SHALL BE PROVIDED IN WELDED CONNECTIONS. 所有节点处需提供3mm角焊缝。
9. TEMPORARY BOLTS SHALL BE RED COATED TO CORROSION FROM THE PERMANENT MOLT. 临时螺栓涂红漆，以防永久氧化。

00	23JUN25	ISSUE FOR FABRICATION	WF	WW	YF	YF
REV	DATE	REVISION	BY	CHKD	APVD	APVD
RETURN TO VENDOR			RESPOND BY			
☐ 1 REVISE AND RESUBMIT						
☐ 2 TO BE ISSUED AS FINAL PROVIDED COMMENTS ARE INCORPORATED						
☐ 3 NOT COMMENT - FINAL ISSUE						
☐ 4 FOR INFORMATION ONLY						
North Field South Project Onshore LNG Facilities						
QatarEnergy LNG						
THIS DOCUMENT IS PROPERTY OF QATAR ENERGY. IT IS THE PROPERTY OF QATAR ENERGY AND NOT BE LOANED, REPRODUCED, COPIED, OR IN ANY MANNER BE USED FOR ANY OTHER THAN THE PURPOSE FOR WHICH IT WAS BEEN PROVIDED, IN WHOLE OR IN PART, IN ANY MANNER WITHOUT THE EXPRESS WRITTEN PERMISSION OF QATAR ENERGY.						
UNITED STEEL STRUCTURES LTD.						
COMPANY CONTRACT NO.: LTGCNFS649821 CONTRACTOR JOB NO.: N/A						
P.O.: 215777C008-00000-PO-1800-20301-NFS620						
REQUISITION NO.: NFS_EPC-TECC-ST-REQ-20301						
EQUIPMENT NAME: PACKAGE - III- STEEL STRUCTURES (Offshore Area)						
TAG NO.: 361-RC3210-S-01						
VENDOR NAME: UNITED STEEL STRUCTURES LTD.						
DOCUMENT CLASS: 3						
VENDOR DOCUMENT NO.: ST20301-02048						
TITLE INLET AREA STEEL STRUCTURE DRAWING 361-RC3210-S-01-CO006						
SCALE 1:10		PROJECT NO. LTGCNFS649821				
PROJECT NFS	PROJECT DOCUMENT NO. 5496_21-ST20301-02045	SHEET No. 1	SIZE A3	REVISION 00		